



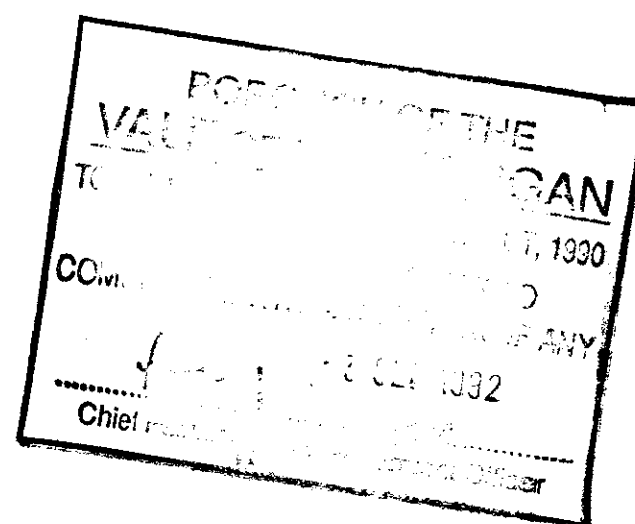

Land to be maintained by
FOREST OF CARDIFF GROUP

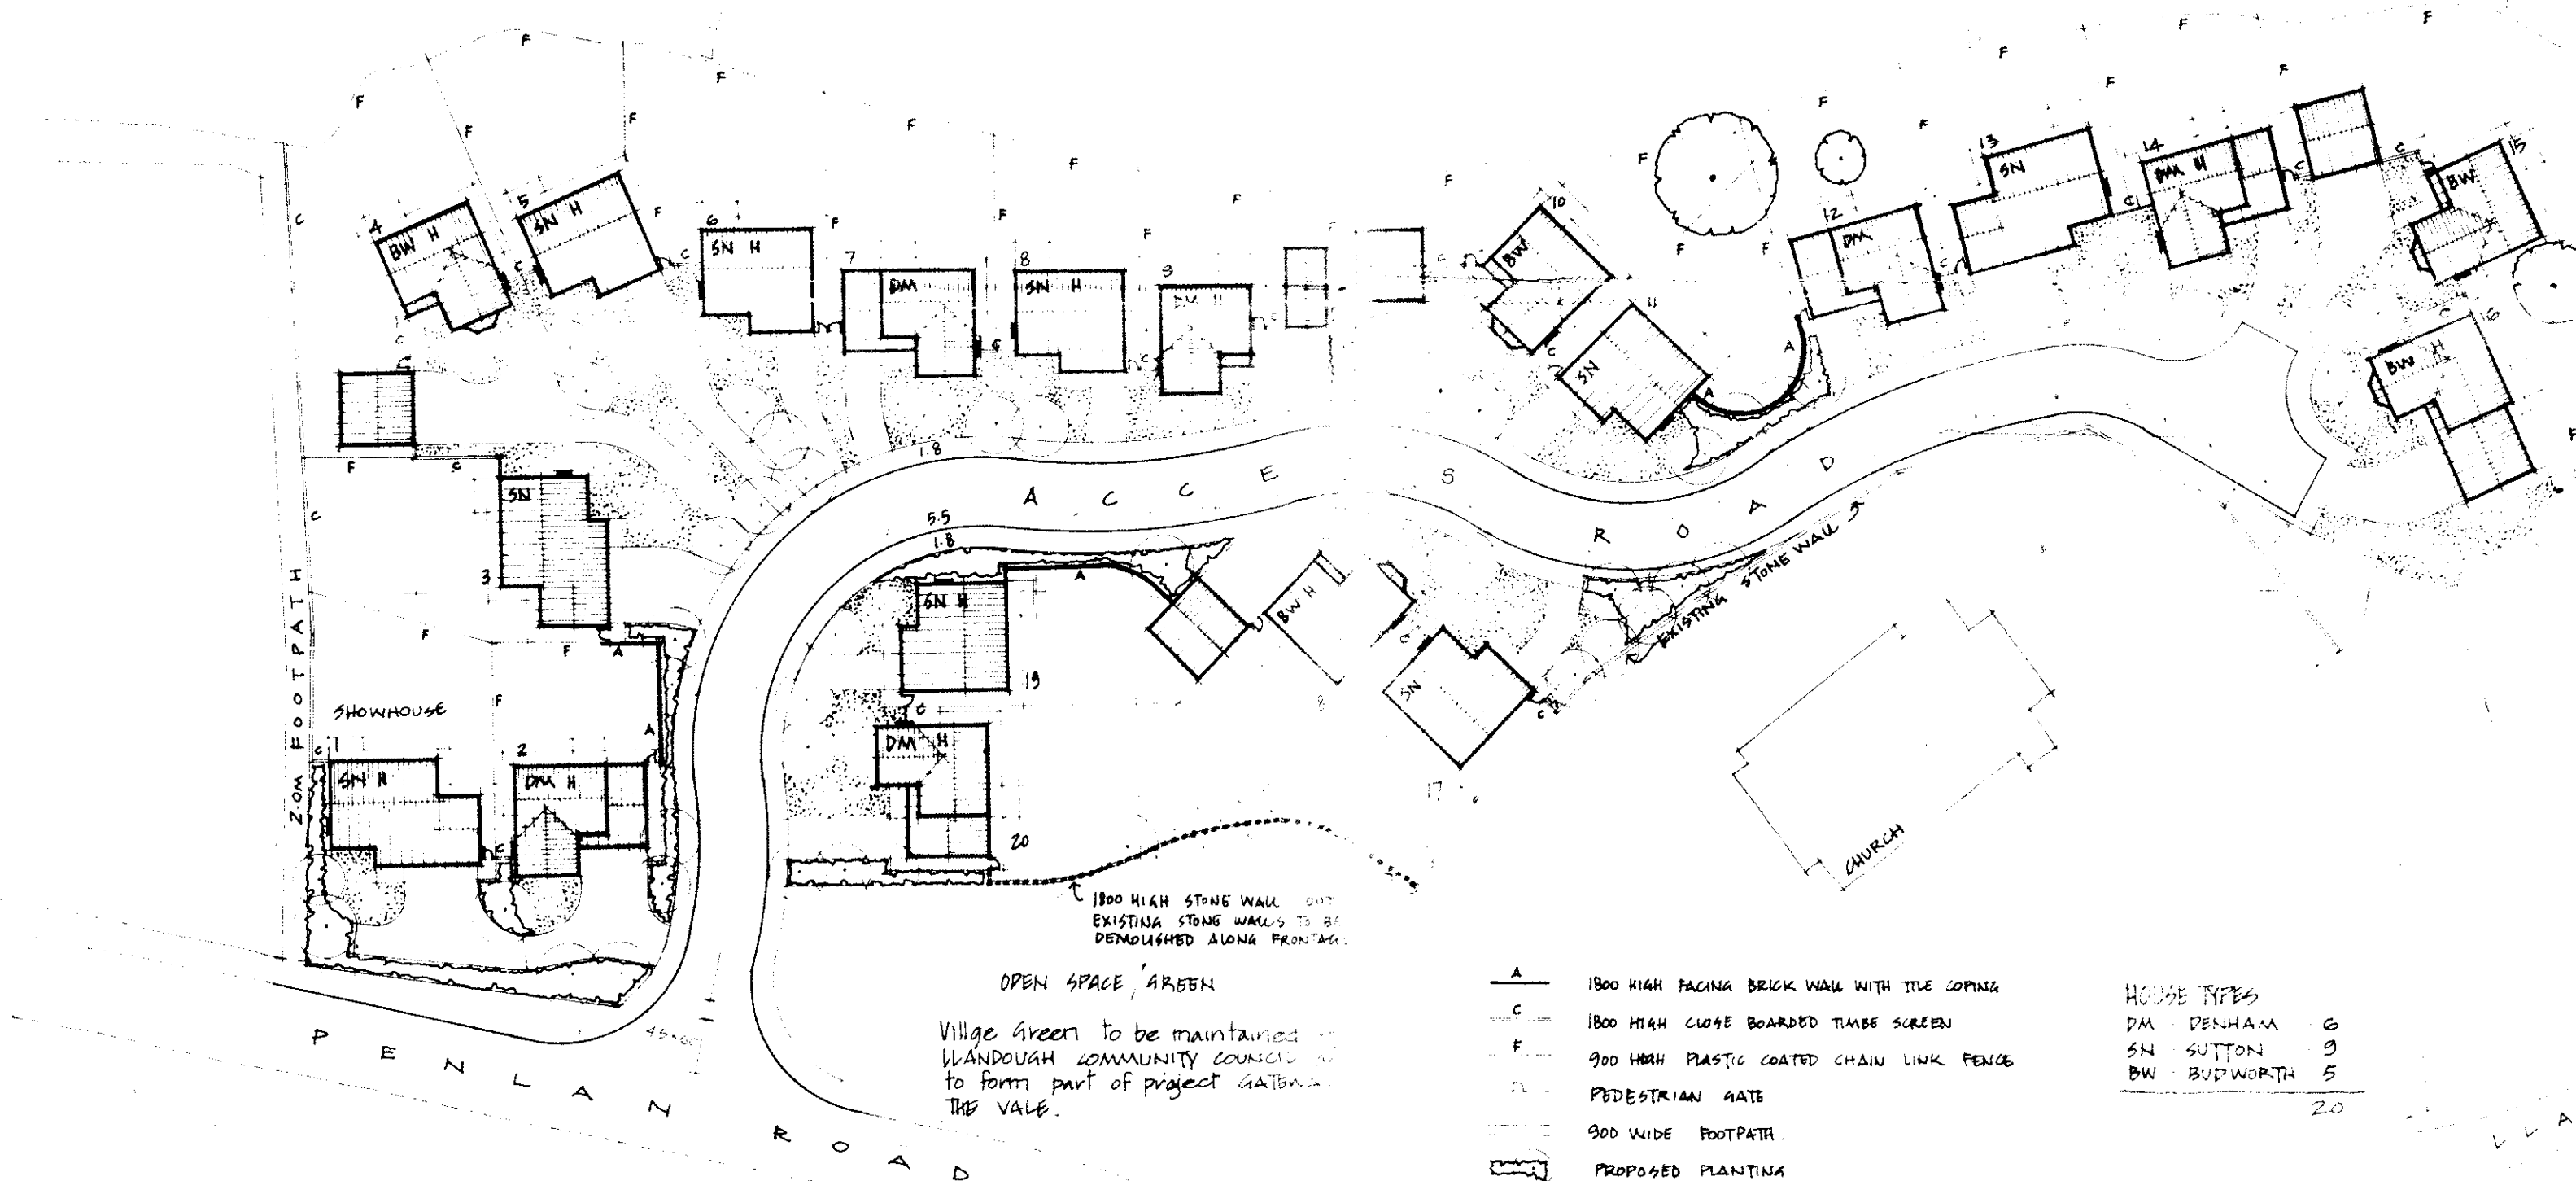


OPEN SPACE / GREEN

Village Green to be maintained by
LLANDOUGH COMMUNITY COUNCIL
to form part of project GATEWAY
THE VALE.

- A 1800 HIGH FACING BRICK WALL WITH TILE COPING
- C 1800 HIGH CLOSE BOARDED TIMBER SCREEN
- F 900 HIGH PLASTIC COATED CHAIN LINK FENCE
- D PEDESTRIAN GATE
- 900 WIDE FOOTPATH
- PROPOSED PLANTING
- TURF BY DEVELOPER
- MANDED PLAN

HOUSE TYPES	
DM - DENHAM	6
SN - SUTTON	9
BW - BUDWORTH	5
	20

REVISIONS

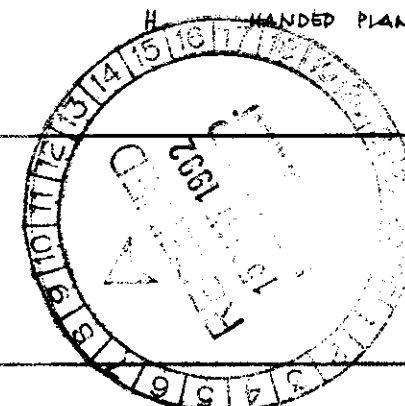


DO NOT SCALE
DIMENSIONS GIVEN IN
THIS DRAWING ARE TO
BE USED FOR CONSTRUCTION

CLIENT IDEAL HOMES WALES
JOB TITLE LLANDOUGH FARM, LLANDOUGH
DRWG TITLE SITE LAYOUT

Drawn Checked Date MAR '02 Scale 1:500 Job 3024 Dwg TP 100


Wyn Thomas+Partners

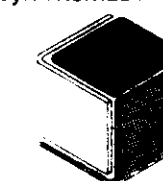

Ideal
Homes

920001/KES

to be maintained by
ST OF CARDIFF GROUP

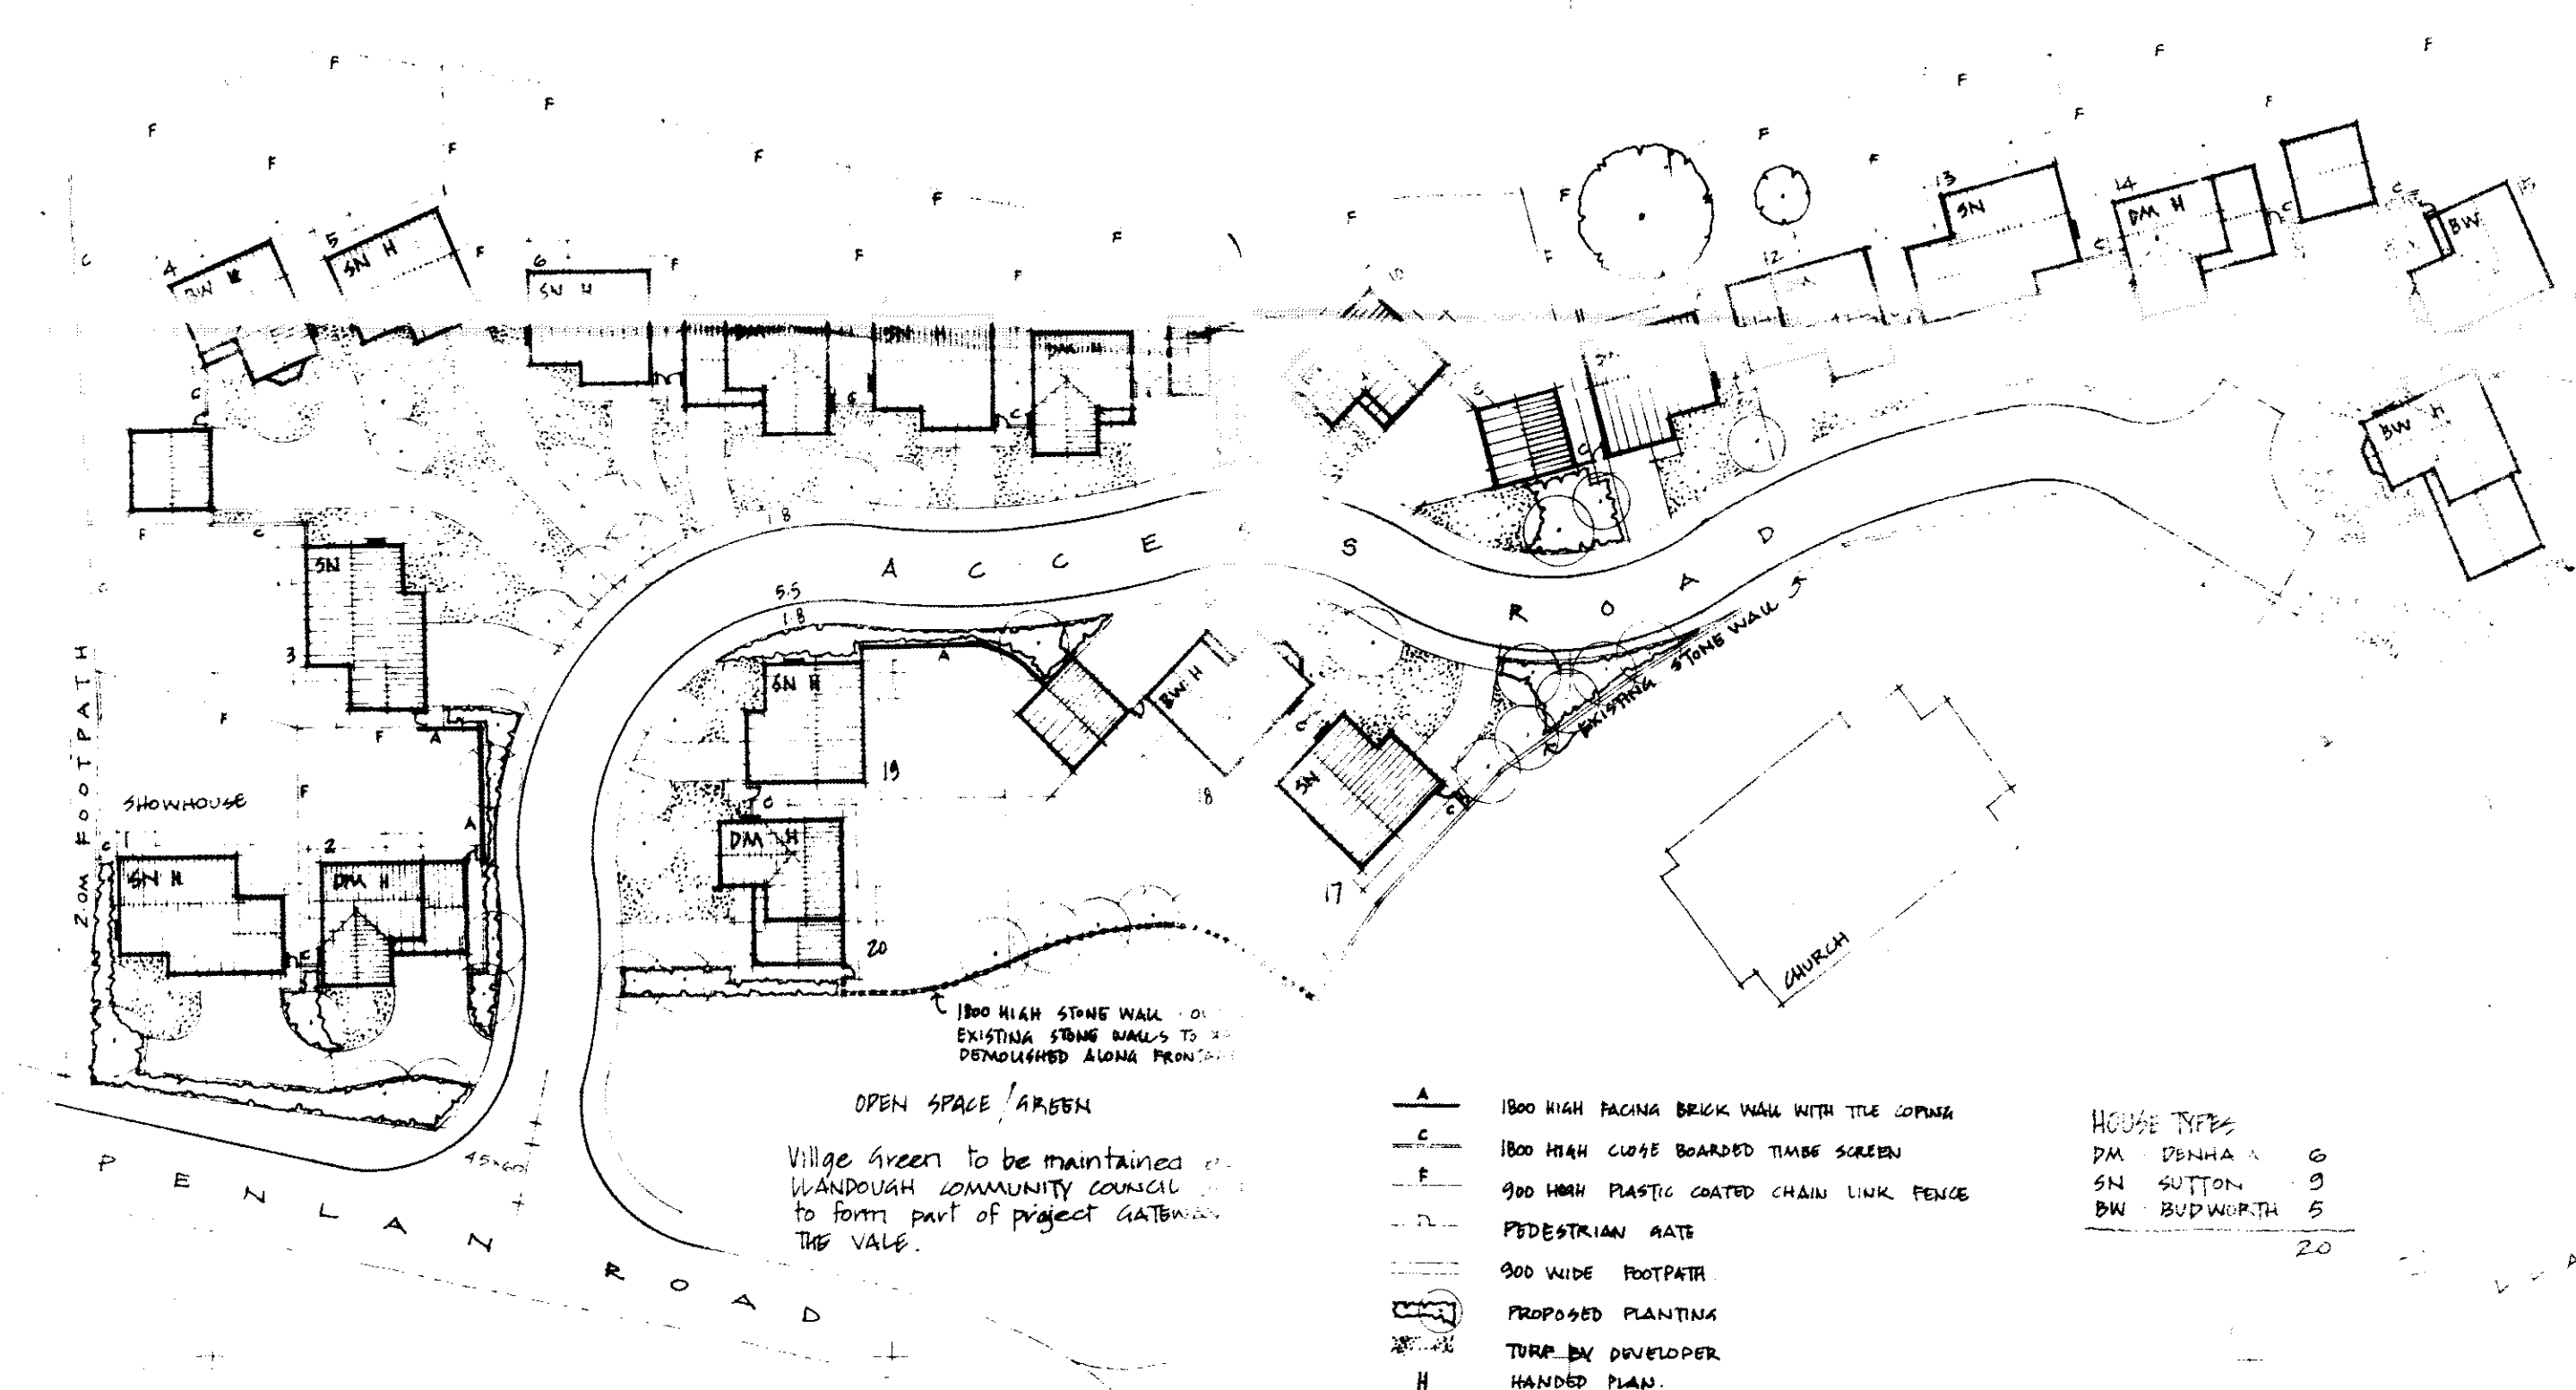


OPEN SPACE / GREEN
Village Green to be maintained by
WLANDOUGH COMMUNITY COUNCIL
to form part of project gateway
into the VALE.

- A 1800 HIGH FACING BRICK WALL WITH TILE COPING
- C 1800 HIGH CLOSE BOARDED TIMBER SCREEN
- F 900 HIGH PLASTIC COATED CHAIN LINK FENCE
- - - PEDESTRIAN RATE
- 900 WIDE FOOTPATH
- PROPOSED PLANTING
- TURF BY DEVELOPER
- H HANDED PLAN

HOUSE TYPES

DM	DENHA	6
SN	SUTTON	9
BW	BUDWORTH	5
		20

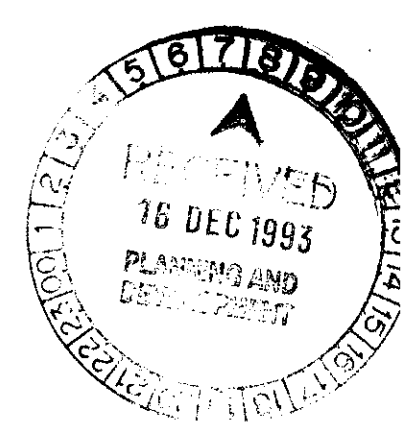

ideal
HOMES

REVISIONS 1. ALL REVISIONS BY A		CLIENT IDEAL HOMES WALES JOB TITLE WLANDOUGH FARM, WLANDOUGH DRWG TITLE SITE LAYOUT		CLIENT IDEAL HOMES WALES JOB TITLE WLANDOUGH FARM, WLANDOUGH DRWG TITLE SITE LAYOUT		Wyn Thomas+Partners 	
Drawn Checked Date Scale Job Dwg R	
Town Planning • Landscape Architects • Architects • Cynllunwyr Dineig • Penseiri Tirwedd • Penseiri Andrews Buildings 67 Queen Street Cardiff CF1 4AU ☎ (0222) 388881 Fax (0222) 385965							

SHRUBS

TREES

PLANT NOS

445

HEAVY STANDARD (H S) (HT 3.5-4.5M, GIRTH 12-14CM)

2 NO BJ BETULA JACQUEMONTII
1 NO CP CRATAEGUS PRUNIFOLIA
1 NO TC TILIA CORDATA

STANDARD (S) (HT 3.0-3.5M, GIRTH 8-10 CM)

6 NO AP ACER PLATANOIDES
7 NO BJ BETULA JACQUEMONTII
4 NO BP BETULA PENDULA
7 NO CP CRATAEGUS PRUNIFOLIA
2 NO SAA SORBUS ARIA LUTESCENS
6 NO SAA SORBUS AUCUPARIA 'ASPLENIFOLIA'
5 NO TC TILIA CORDATA

FEATHERED (F) (HT 1.8-2.4M)

8 NO AP ACER PLATANOIDES
5 NO BJ BETULA JACQUEMONTII
12 NO BP BETULA PENDULA
3 NO CP CRATAEGUS PRUNIFOLIA
3 NO SAA SORBUS ARIA LUTESCENS
2 NO SAA SORBUS AUCUPARIA 'ASPLENIFOLIA'
6 NO TC TILIA CORDATA
3 NO AP (1 NO S, 1 NO F)
2 NO CP (1 NO S, 1 NO F)


3 NO TC (1 NO S, 2 NO F)

3 NO TC (1 NO S)

2 NO CP (S)

4 NO BP (F)

2 NO CP (1 NO S, 1 NO F)

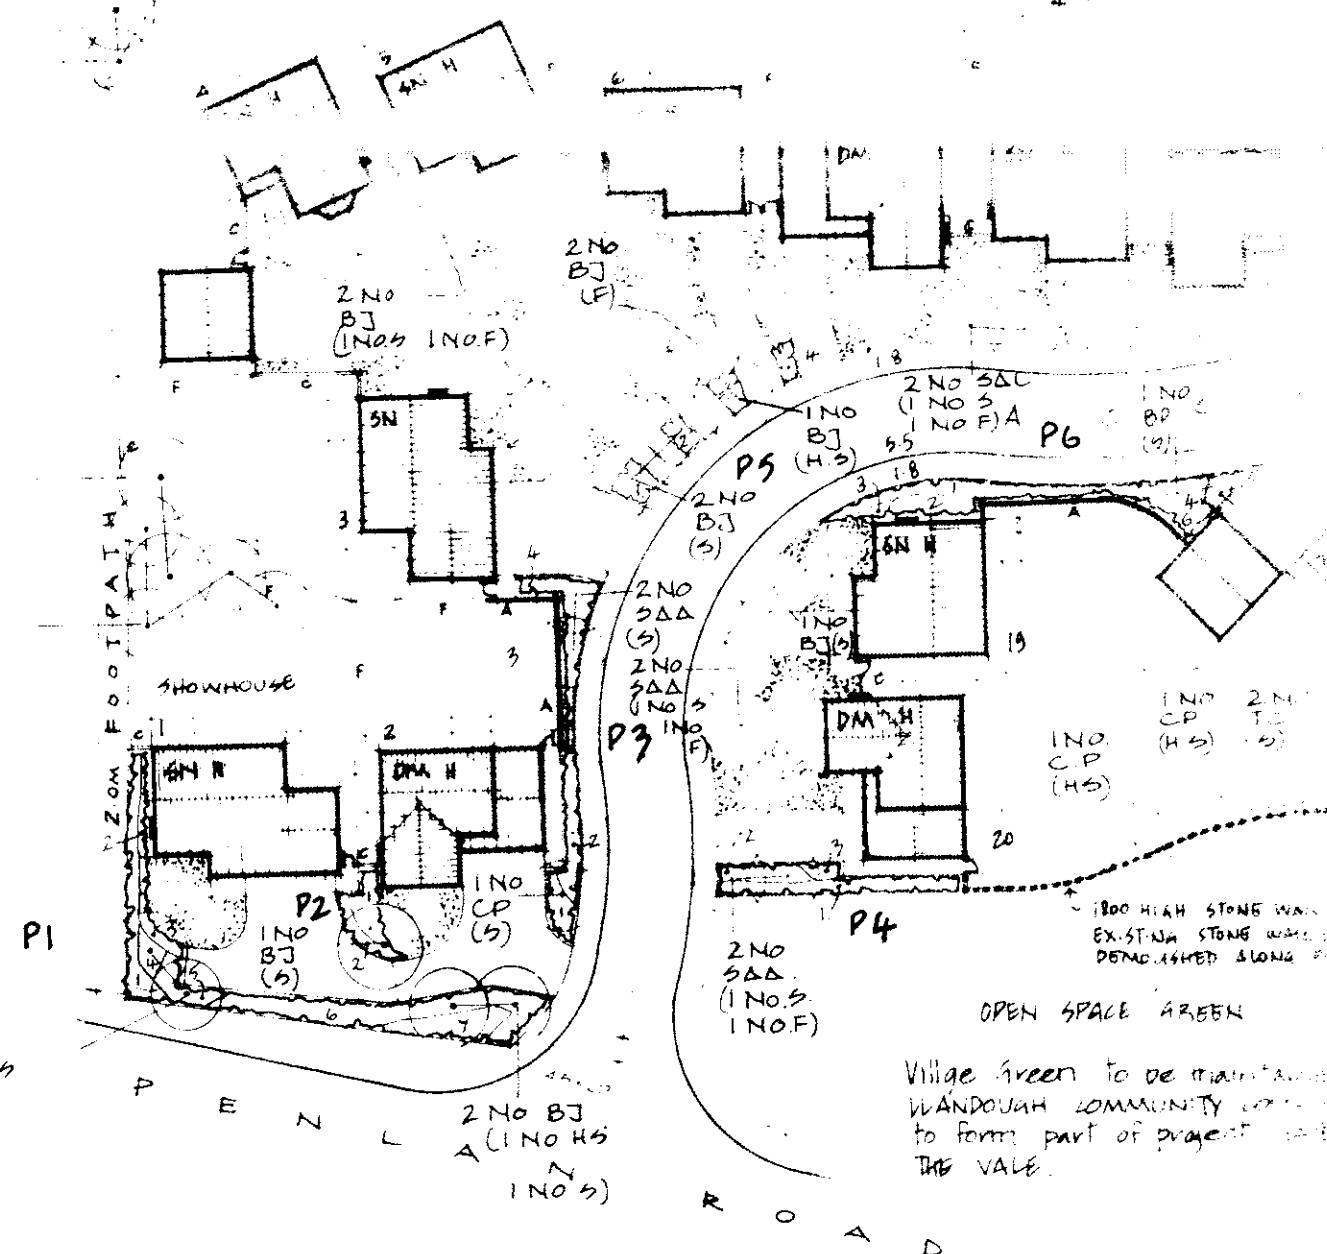

Village Green to be maintained by LLANDOUGH COMMUNITY to form part of project with the VILLAGE.

SHRUBS

P1 1 ESCALLONIA DONARD SEEDLING
2 HEBE
3 HEBE
4 ILEX
5 BERBERIS
6 ATRORHIZA
7 PRUNUS
8 BERBERIS
9 ATRORHIZA

P2 1 BERBERIS
2 HEBE

P3 1 PRUNUS
2 ESCALLONIA
3 PARTHENSIS
4 COTONEASTER DECORUS

36 NO
7 NO
14 NO
8 NO

28 NO
52 NO
36 NO

24 NO
20 NO

12 NO
20 NO
2 NO
52 NO

P4 1 ESCALLONIA DONARD SEEDLING
2 COTONEASTER CONSPICUUS
DECORUS
3 PHILADELPHUS VIRGINAL

32 NO
12 NO
4 NO

P5 1 COTONEASTER CONSPICUUS DEC.
2 COTONEASTER CONSPICUUS DEC.
3 COTONEASTER CONSPICUUS DEC.
4 COTONEASTER CONSPICUUS DEC.

16 NO
12 NO
16 NO
12 NO

P6 1 COTONEASTER CONSPICUUS DEC.
2 PYRACANTHA 'ORANGE GLOW'
3 PHILADELPHUS VIRGINAL
4 ILEX AQUIFOLIUM
5 BERBERIS THUNBERGII
6 ATRORHIZA
7 CLEMATIS MONTANA 'RUBENS'

104 NO
15 NO
4 NO
4 NO
8 NO
12 NO
2 NO

P7 1 POTENTILLA TANGERINE
2 CORNUS ALBA 'SIBIRICA'
3 STEPHANDRA INCISA 'CRISPA'

24 NO
4 NO
16 NO

P8 1 COTONEASTER CONSPICUUS
DECORUS
2 STEPHANDRA INCISA 'CRISPA'
3 ROSA FRAU DAGMAR HASTRUP
4 POTENTILLA TANGERINE

40 NO
12 NO
24 NO
8 NO

P9 1 COTONEASTER CONSPICUUS
DECORUS
2 ROSA FRAU DAGMAR HASTRUP
3 STEPHANDRA INCISA 'CRISPA'
4 PARTHENSIS HENRYANA

48 NO
18 NO
16 NO
1 NO

P10 1 CORNUS ALBA 'SIBIRICA'
2 PHILADELPHUS VIRGINAL
3 PRUNUS LAURO CERACUS
OTTO LUYKEN
4 POTENTILLA TANGERINE

18 NO
2 NO
10 NO
8 NO

P11 1 CORNUS ALBA 'SIBIRICA'
2 PHILADELPHUS VIRGINAL
3 PRUNUS LAURO CERACUS
OTTO LUYKEN
4 POTENTILLA TANGERINE

18 NO
2 NO
10 NO
8 NO

GENERAL NOTES:

Exact position of trees to be determined by the client or the client's agent.
If substitution is required, the client must be notified in writing and the client must be responsible for the cost of the substitution.
Plants to be planted in accordance with the client's requirements.
All planted areas to be covered by 50mm thick mulch.
Cult to be 500mm depth in planted areas.

PRUNUS LAURO CERACUS
OTTO LUYKEN
CORNUS ALBA 'SIBIRICA'
ILEX AQUIFOLIUM
POTENTILLA TANGERINE

5 NO BP
(1 NO S, 4 NO F)

8 NO


12 NO

4 NO

10 NO

3 NO TC
(1 NO S, 2 NO F)

3 NO BP
(1 NO S, 1 NO F)

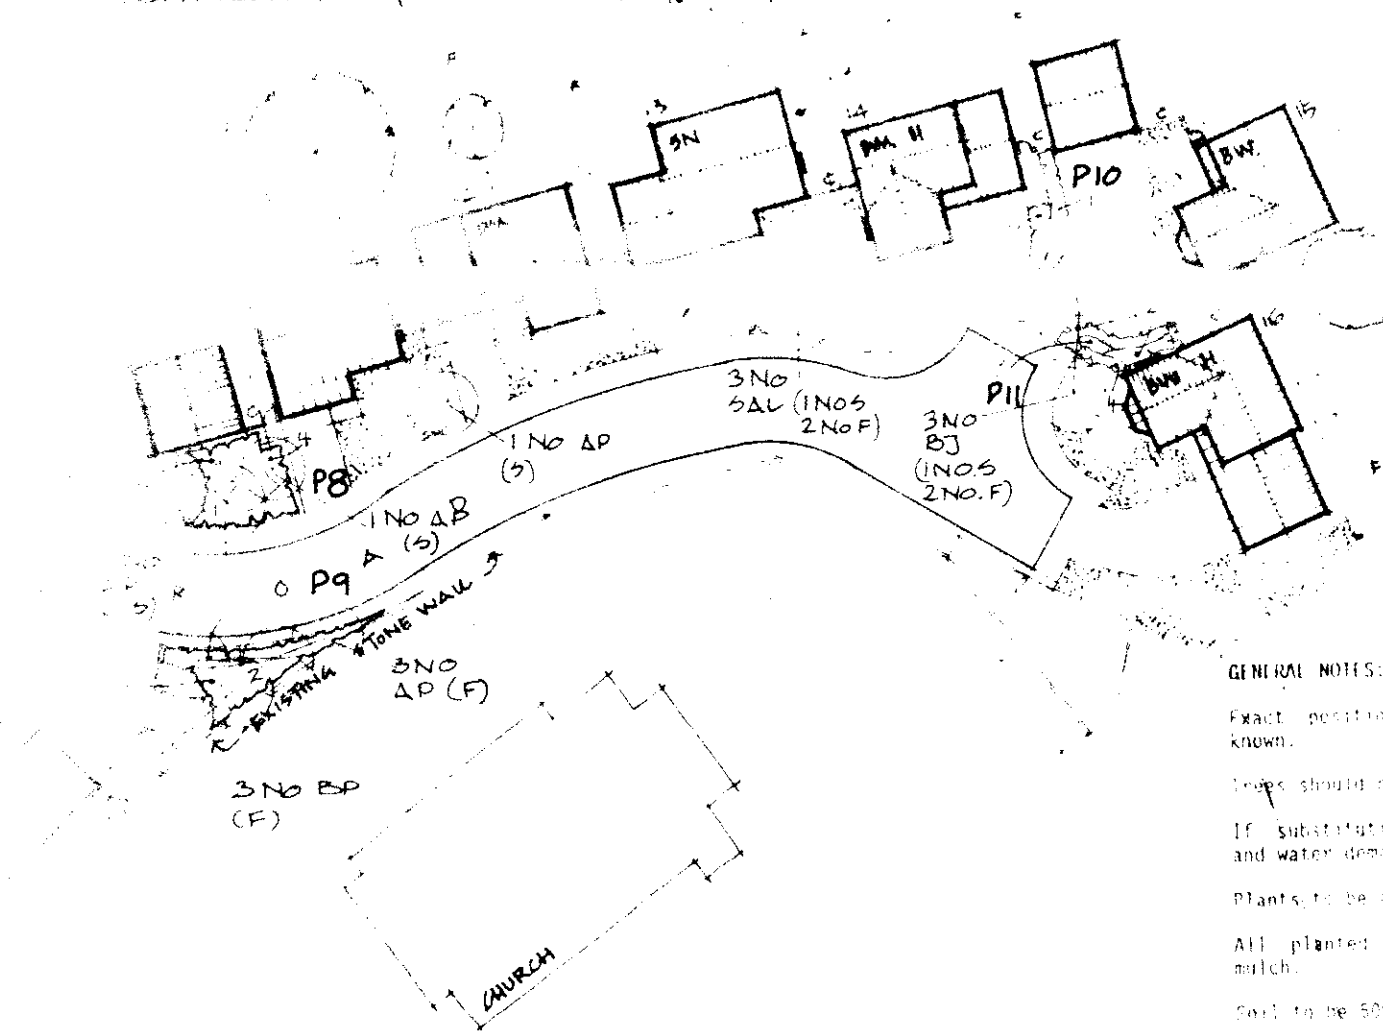


1800 HIGH FACING BRICK WALL WITH TILE COPING
1800 HIGH CLOSE BOARDED TIMBER SCREEN
900 HIGH PLASTIC COATED CHAIN LINK FENCE
PEDESTRIAN GATE
900 WIDE FOOTPATH
PROPOSED PLANTING
TURF BY DEVELOPER
HANDLED PLAN
GRASS - TARMAC WITH CONC. EDGE
PAVING - CONC. SLABS
FOOTPATH - TARMAC

HOUSE TYPES
PM DENHAM 6
SN SUTTON 9
BW BUDWORTH 5
20

REVISIONS

CLIENT	IDEAL HOMES WALES
JOB TITLE	LLANDOUGH FARM, LLANDOUGH
DRWG TITLE	PLANTING PROPOSALS
Drawn	MP.
Checked	
Date	01. 94.
Scale	1:500
Job	3024
Dwg	TP 100 (L)

Town Planners - Landscape Architects - Architects - Cynllunwyr Dineig - Penryn Tinned - Penryn
Andrews Buildings - 67 Queen Street - Cardiff CF1 4AU - Tel (0222) 398881 - Fax (0222) 398885

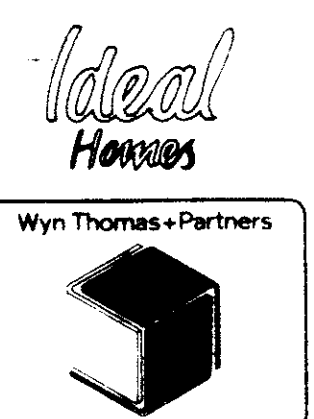

1. All house drains are to be installed in cast-iron pipes with PVC manholes, manholes, and traps where indicated.

1800

m.h. cover

inlet pipe

1200 dia.

STREET LIGHTING COLUMN

2.0M FOOTPATH

SHOWHOUSE

OPEN SPACE

P R Z L A Z P O A D

CHURCH

6m. sewer easment

EX. MH
CL 29.01
LL 27.61

RECEIVED
23 DEC 1993
PLANNING AND
DEVELOPMENT

REVISIONS


DO NOT SCALE
Dimensions must be verified
by your customer on site. If

CLIENT	IDEAL HOMES WALES
JOB TITLE	LLANDOUGH FARM, LLANDOUGH
DRWG TITLE	drainage and highway details



Drawn	Checked	Date MAR-92	Scale 1/200	Job 3024	Dwg E100/1	N
-------	---------	----------------	----------------	-------------	---------------	---

Town Planners • Landscape Architects • Architects • Cynllunwyr Dinodig • Penodol Tîrnod • Penodol
Andrews Buildings, 67 Queen Street, Cardiff CF1 4AU. Tel (0222) 309551 Fax (0222) 309550

Wyn Thomas+Partners

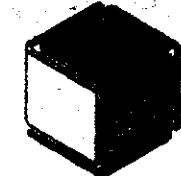

NOTES:
All dimensions must be checked on site and not scaled from this drawing

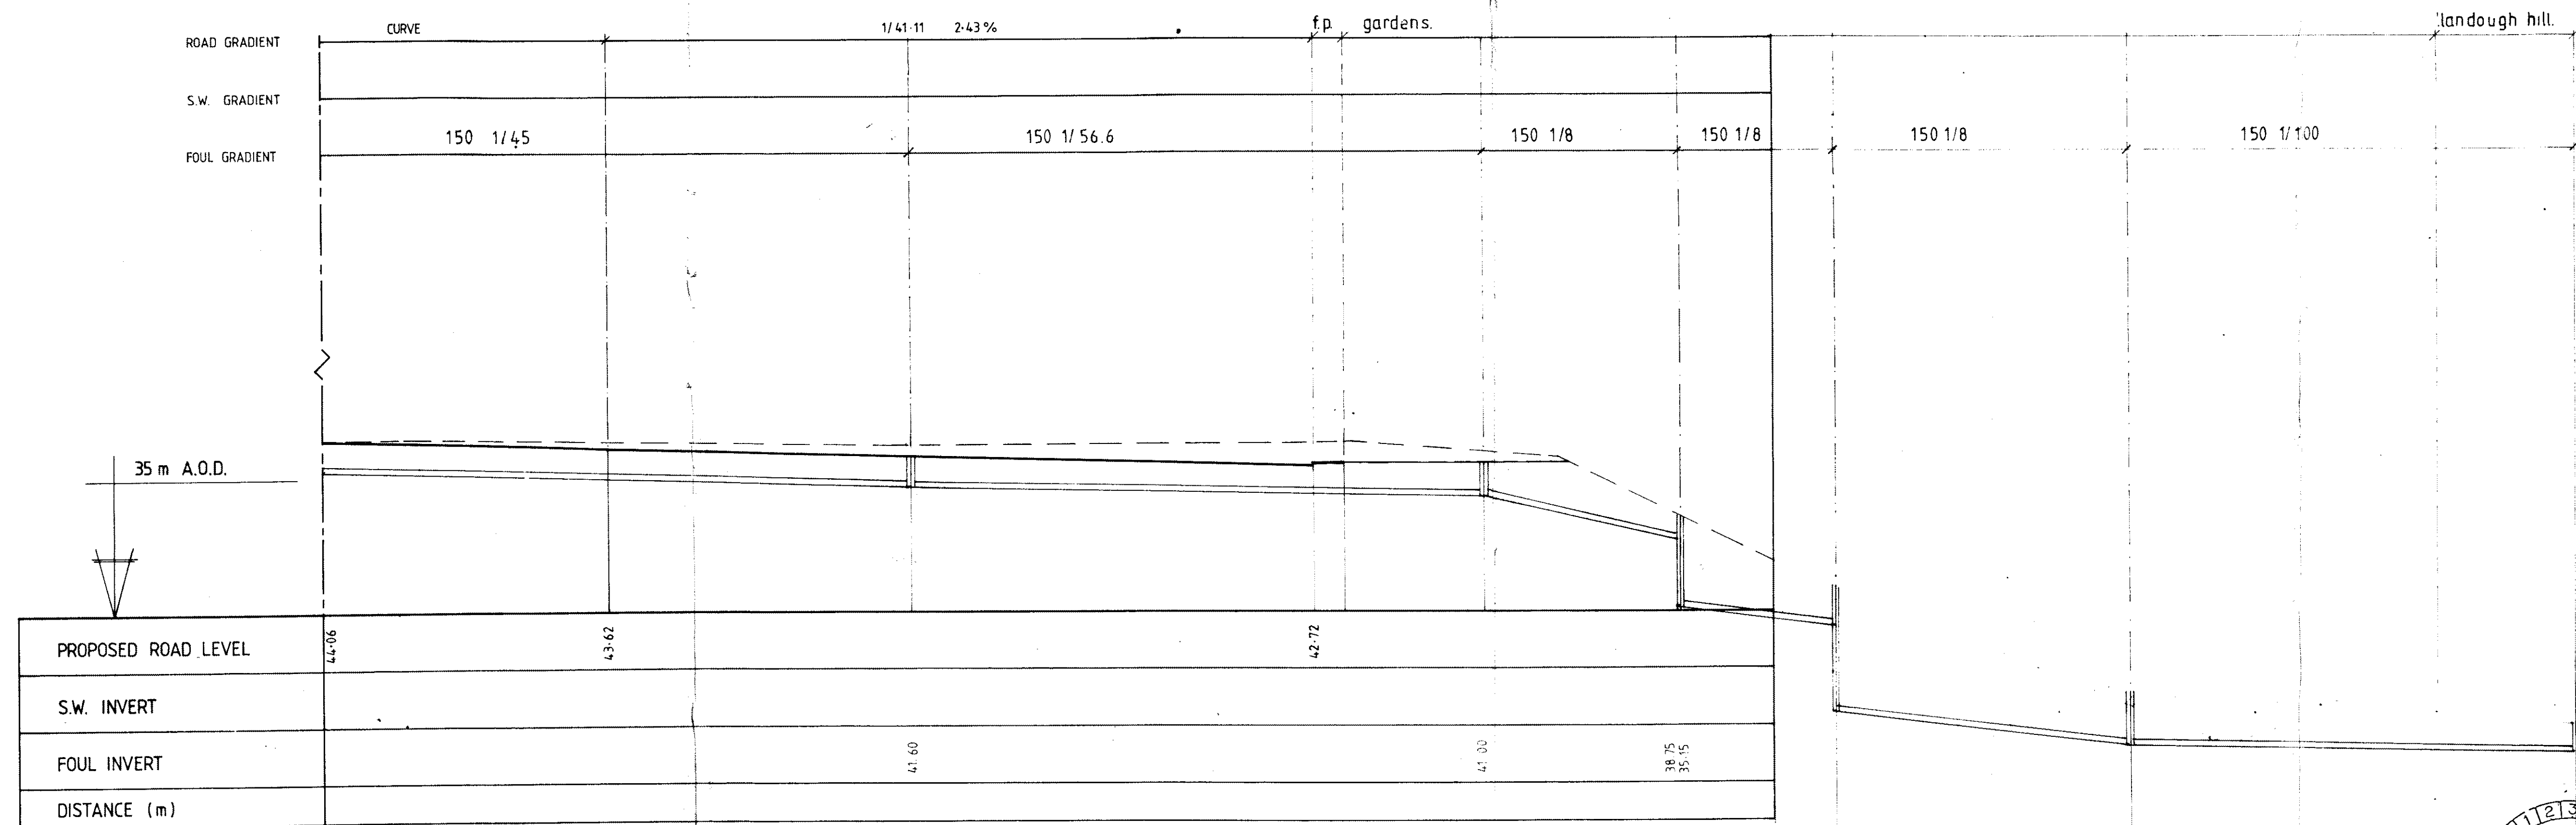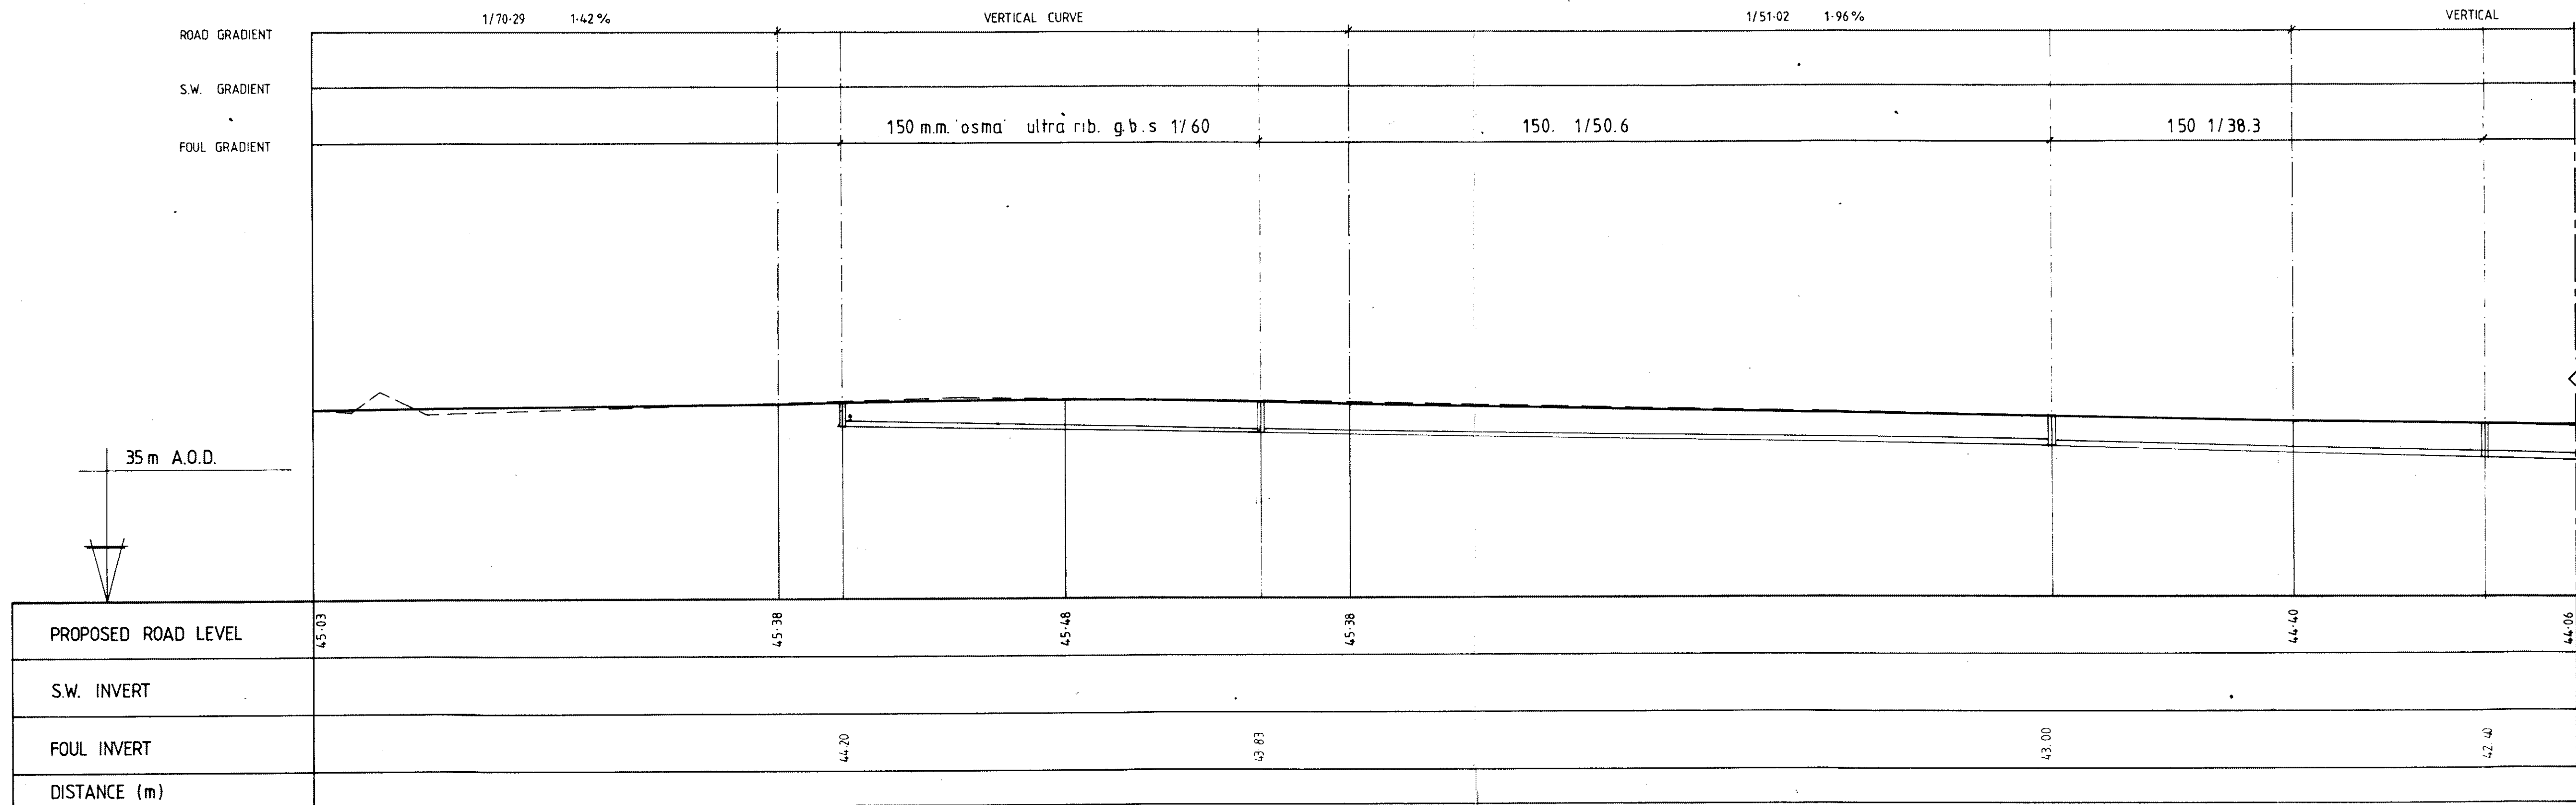

© copyright

Client

Job Title
GREAT HOUSE FARM, LLANDOUGH,
PENARTH.

Drawing Title
LONGITUDINAL ROAD AND
DRAINAGE SECTIONS.


Scale 1:200

Date MAR '92 Drawn by N.R.


Drw. No. E 100/2 Rev.



SECTION 1.

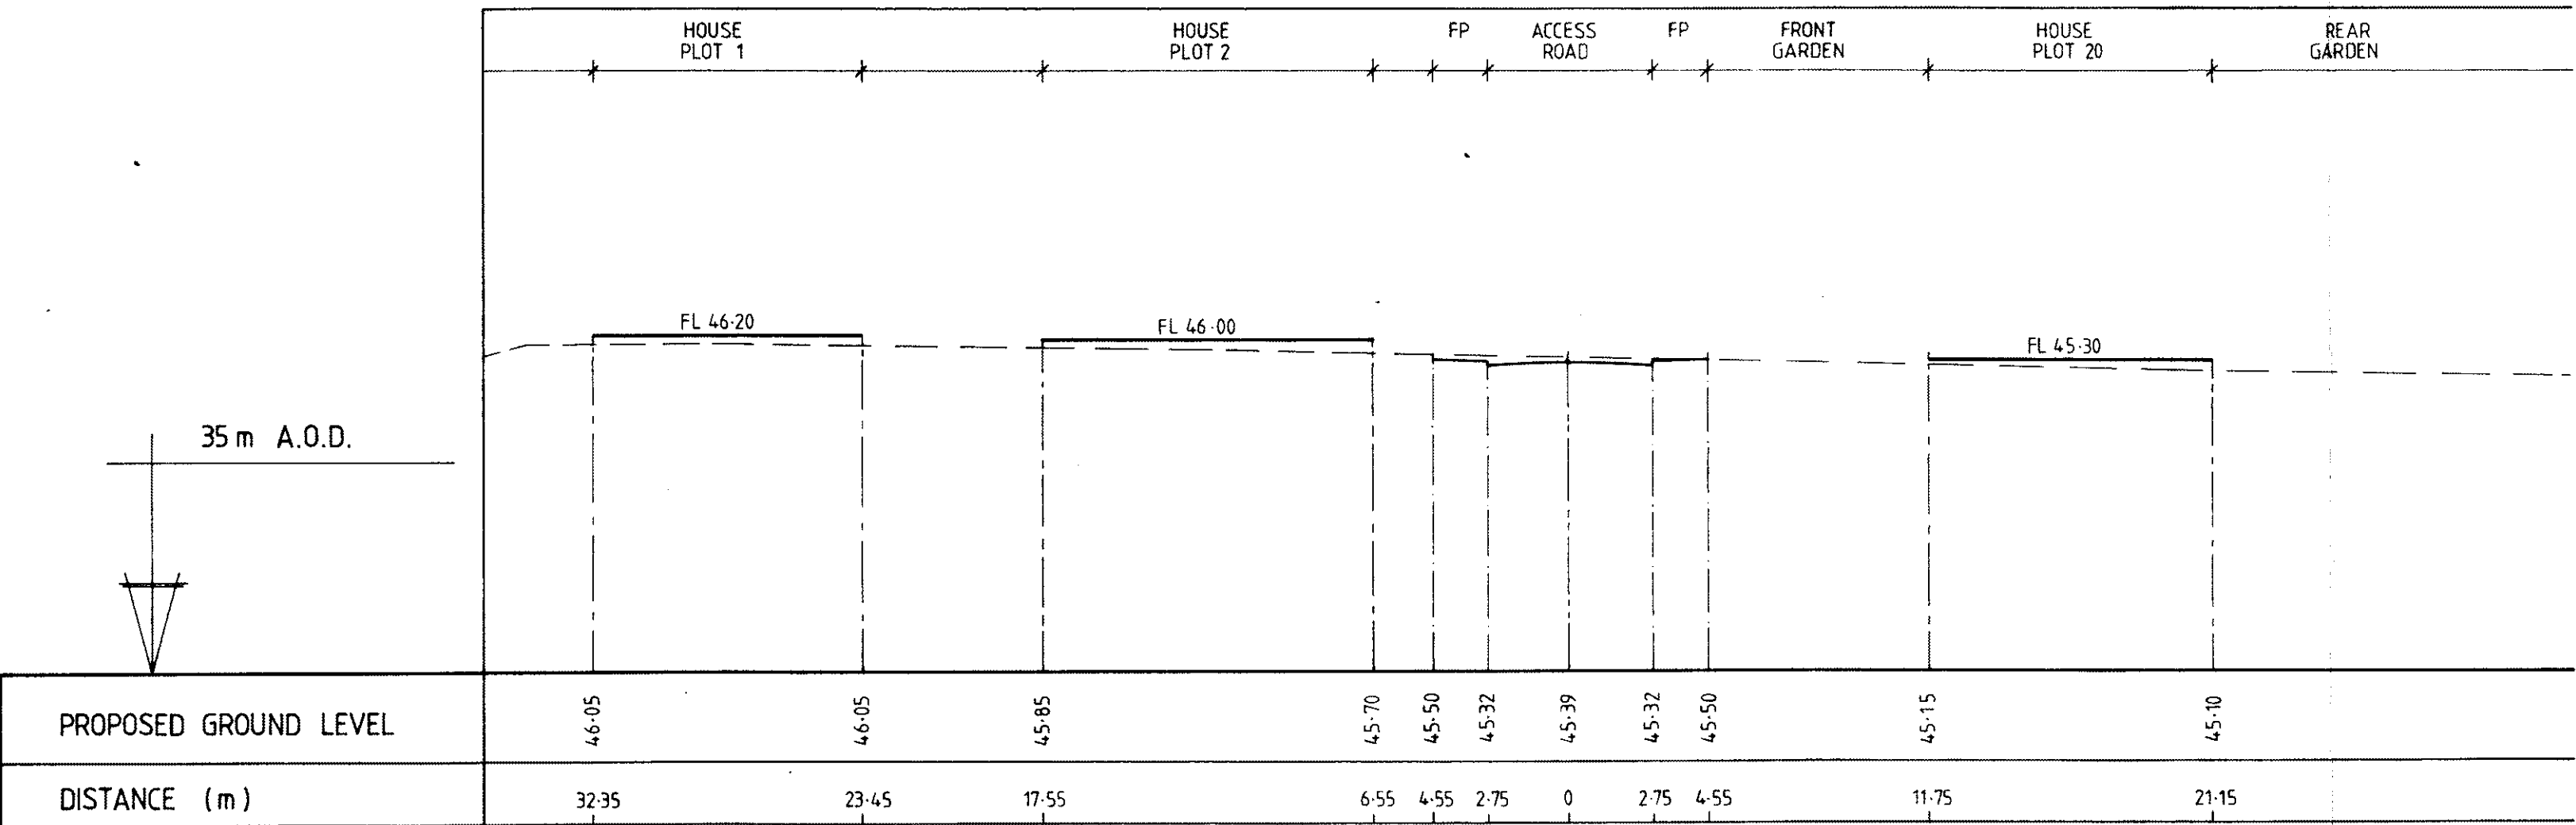

SECTION 2.

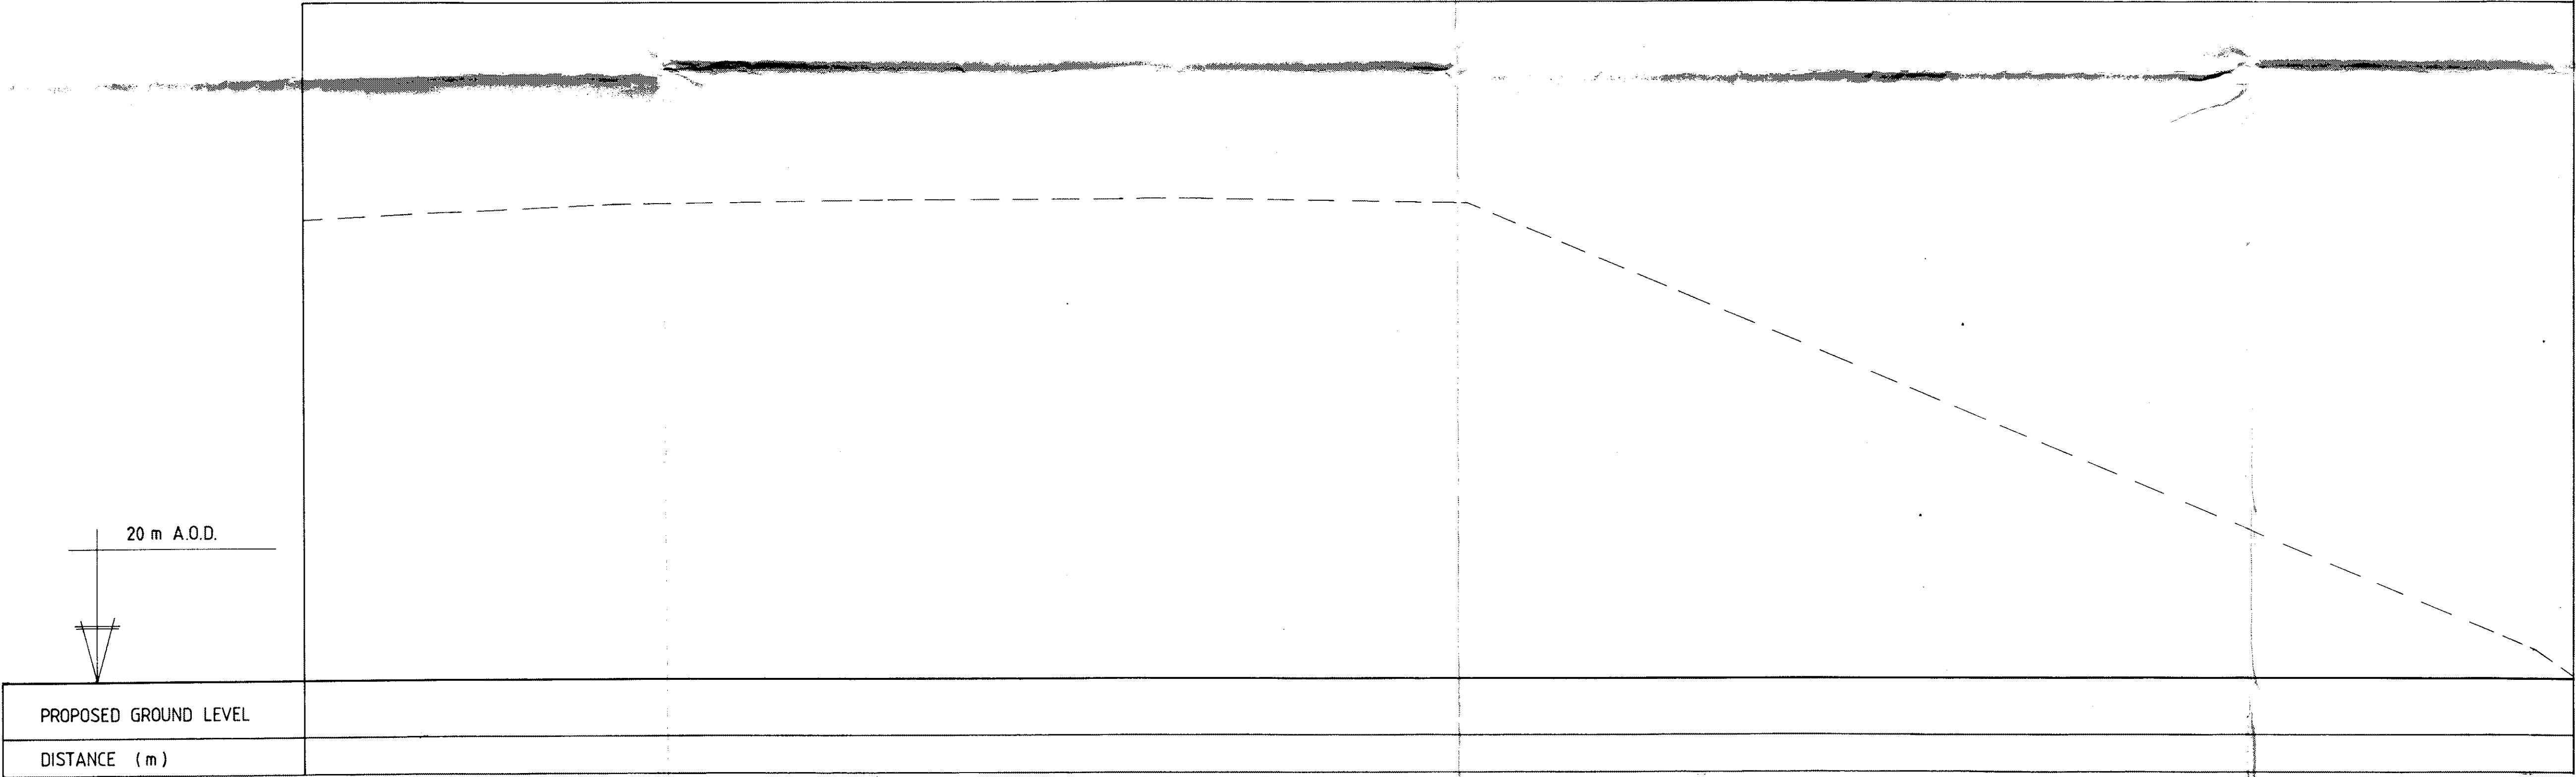

NOTES:
All dimensions must be checked on site and not scaled from this drawing

A		
	Date	Revisions

© copyright

Client

Job Title

GREAT HOUSE FARM, LLANDOUGH,
PENARTH.


Drawing Title

ACCESS ROAD AND HOUSE
CROSS SECTIONS.


Scale 1:200

Date MAR '92 Drawn by N.R.


Drg. No. E 100 / 3 Rev.

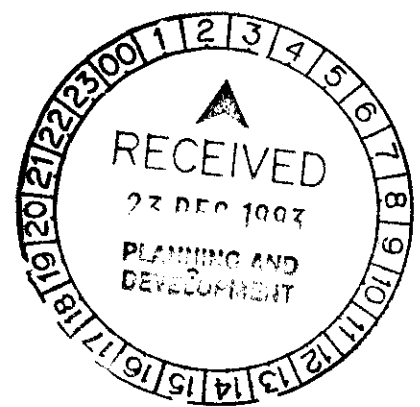

SECTION 3.

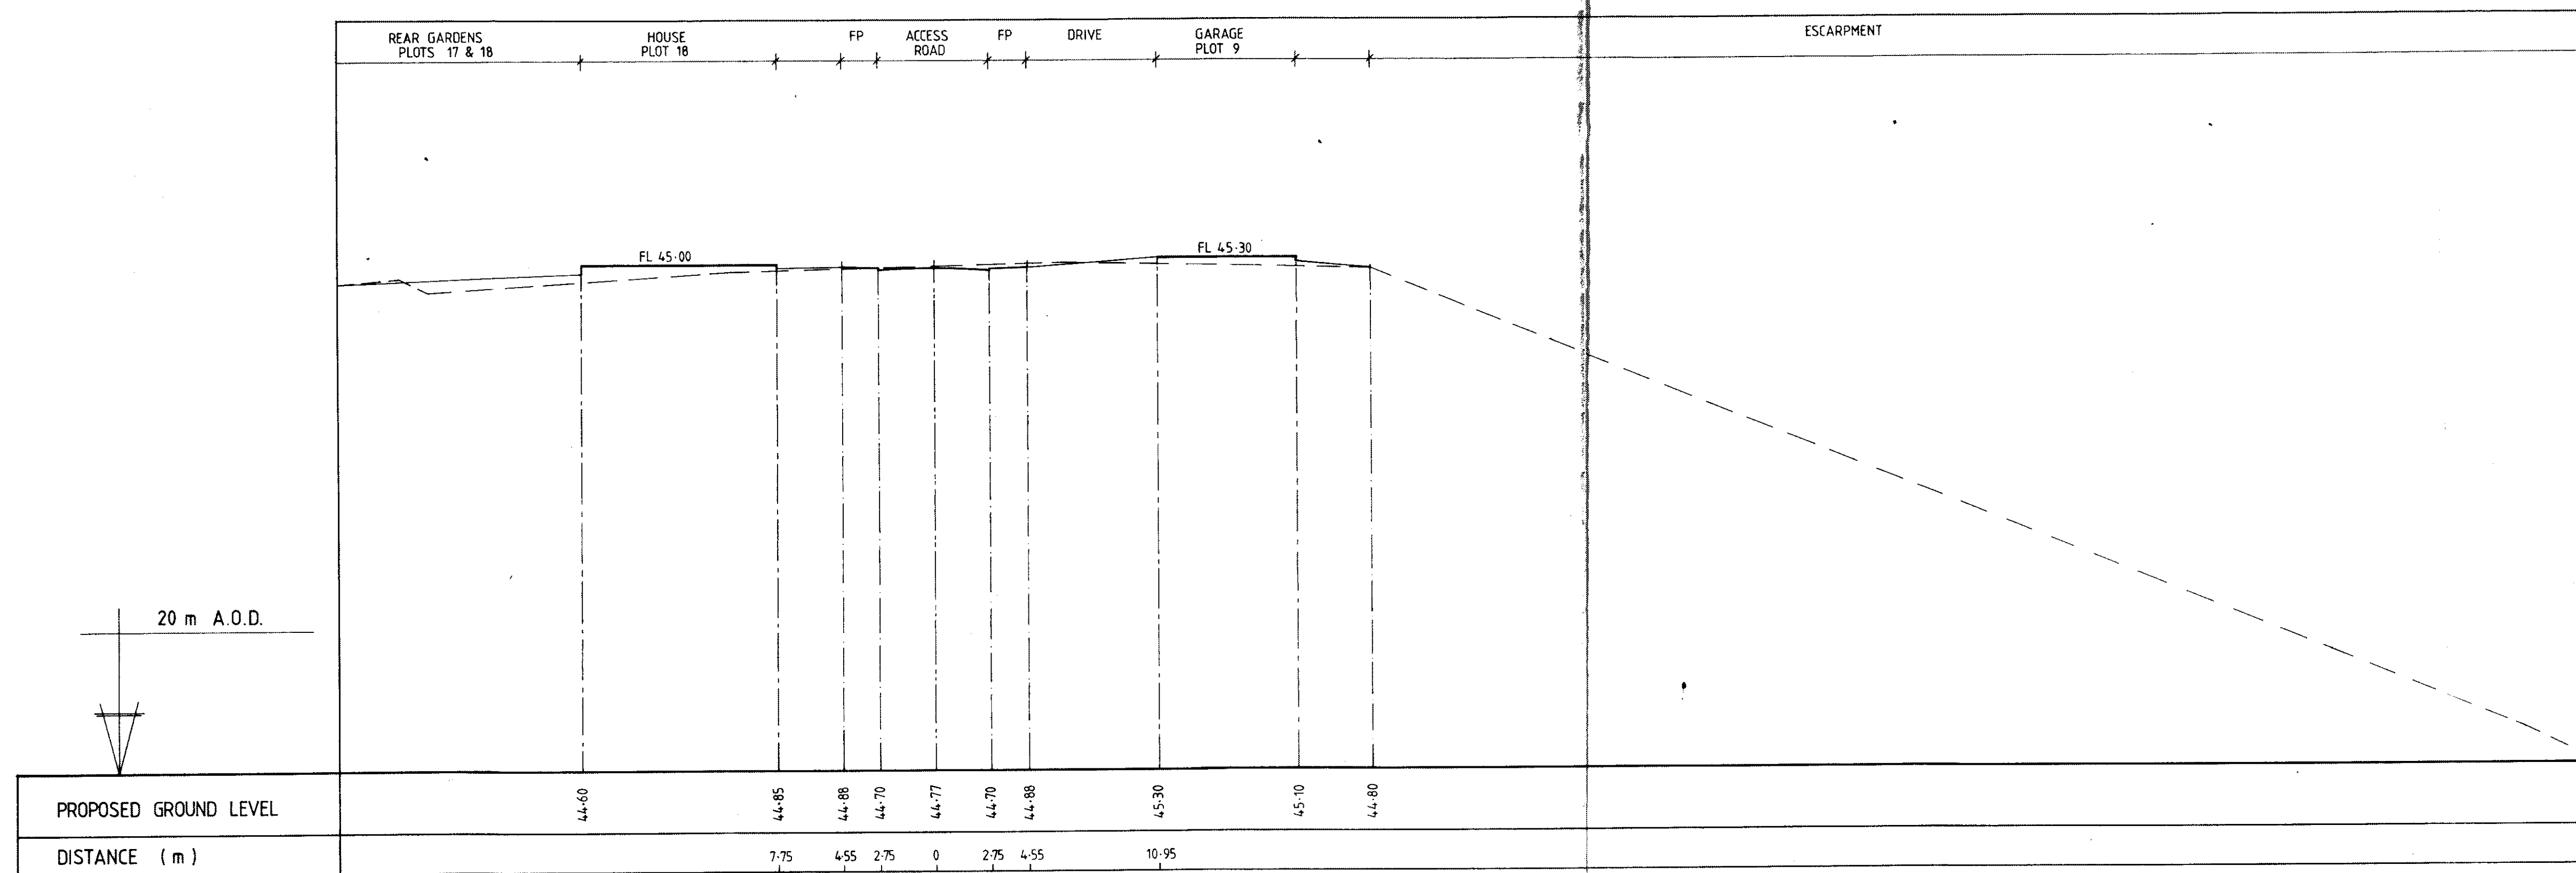

SECTION 4.

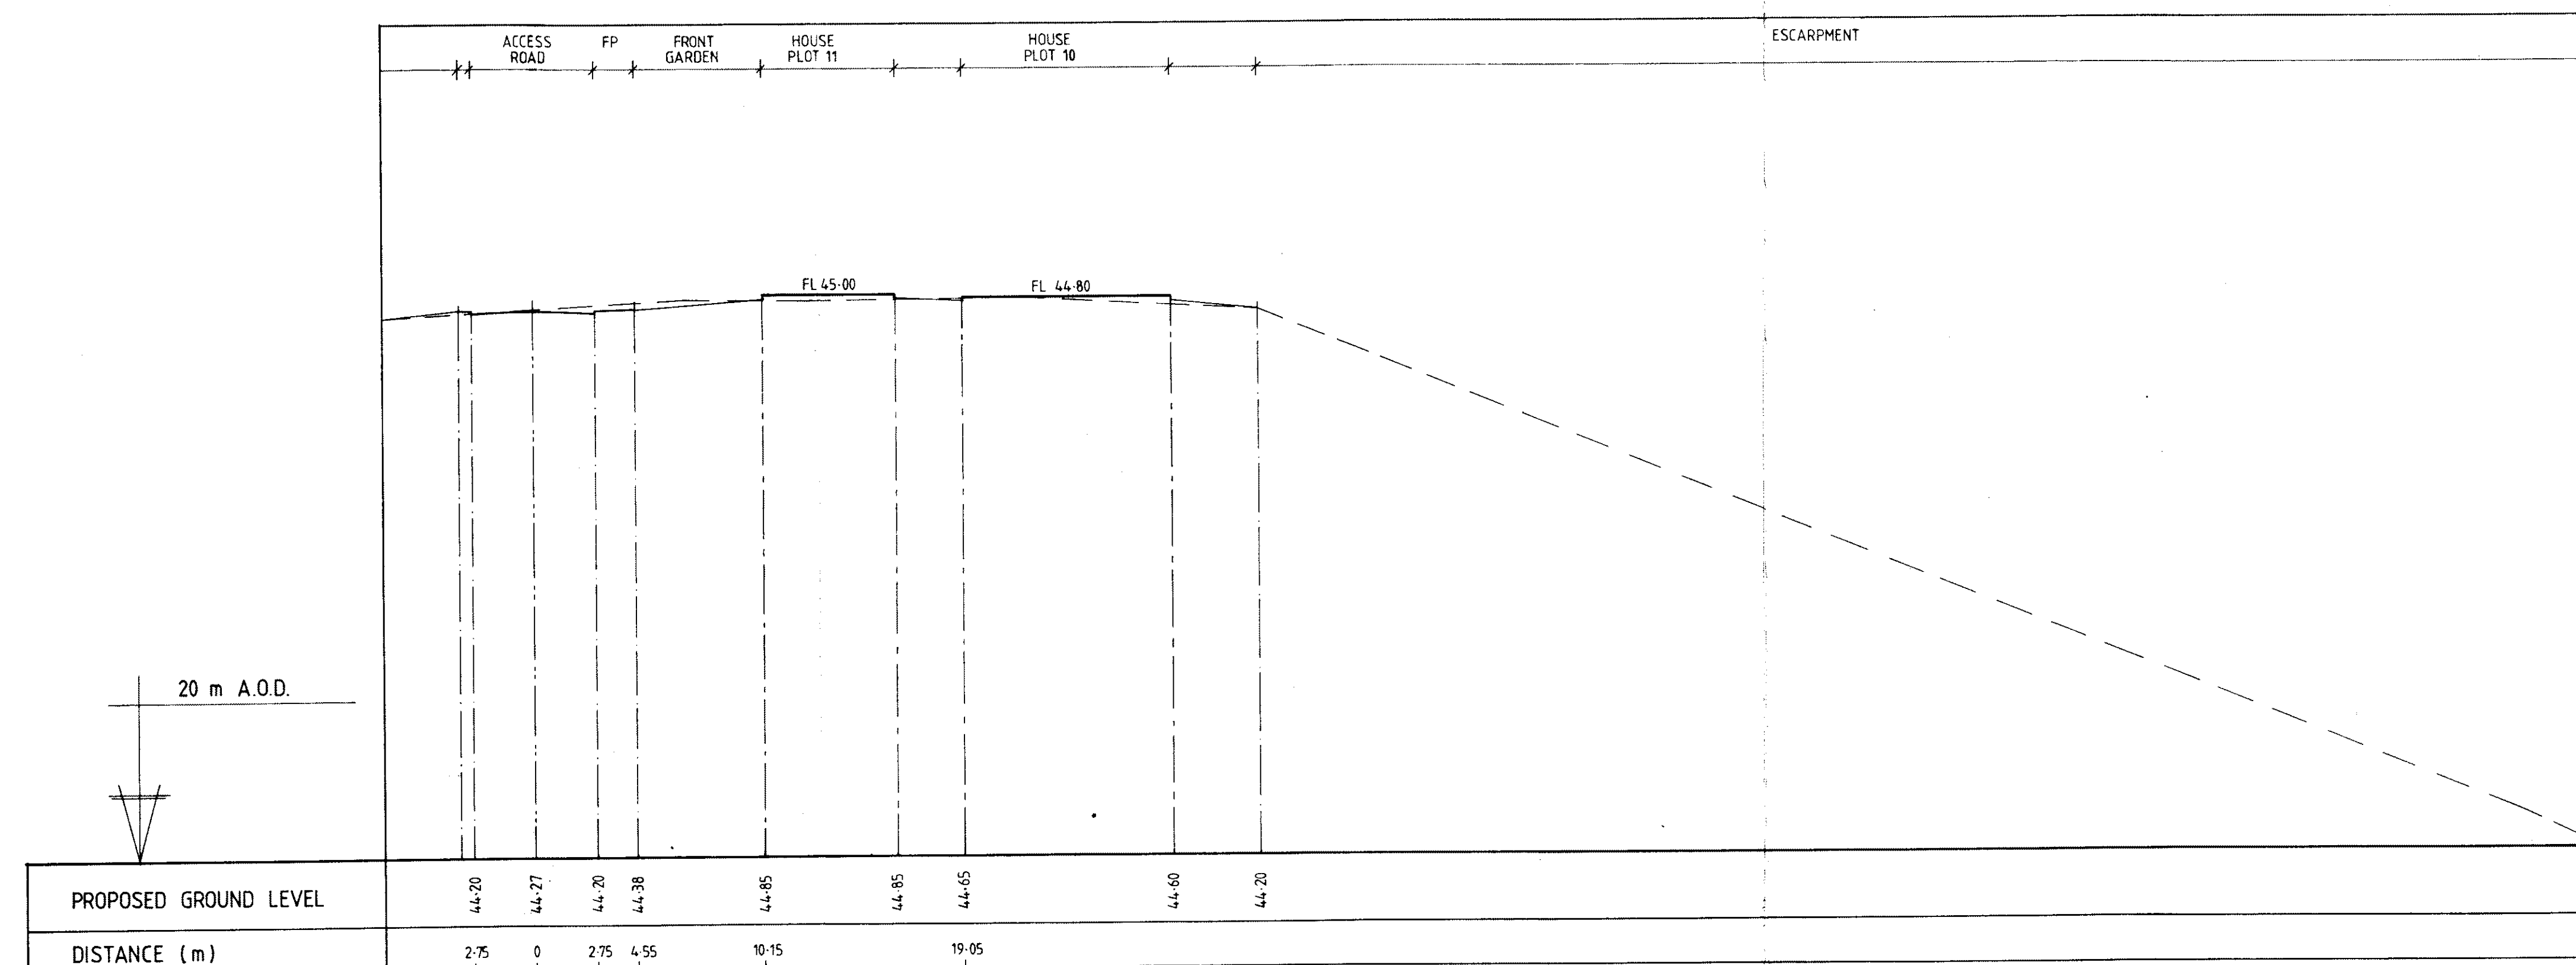

NOTES:

All dimensions must be checked on site and not scaled from this drawing.

© copyright

Client

Job Title

GREAT HOUSE FARM, LLANDOUGH,
PENARTH.

Drawing Title

ACCESS ROAD AND HOUSE
CROSS SECTIONS.

Scale 1 : 200

Date	MAR '92	Drawn by	N.R.
------	---------	----------	------

Drg. No. E 100 / 4.


ay

A PRODUCT OF THE UNO RANGE - ARCHITECT CAT No 7311


94 x 841mm

A1

SECTION 5.

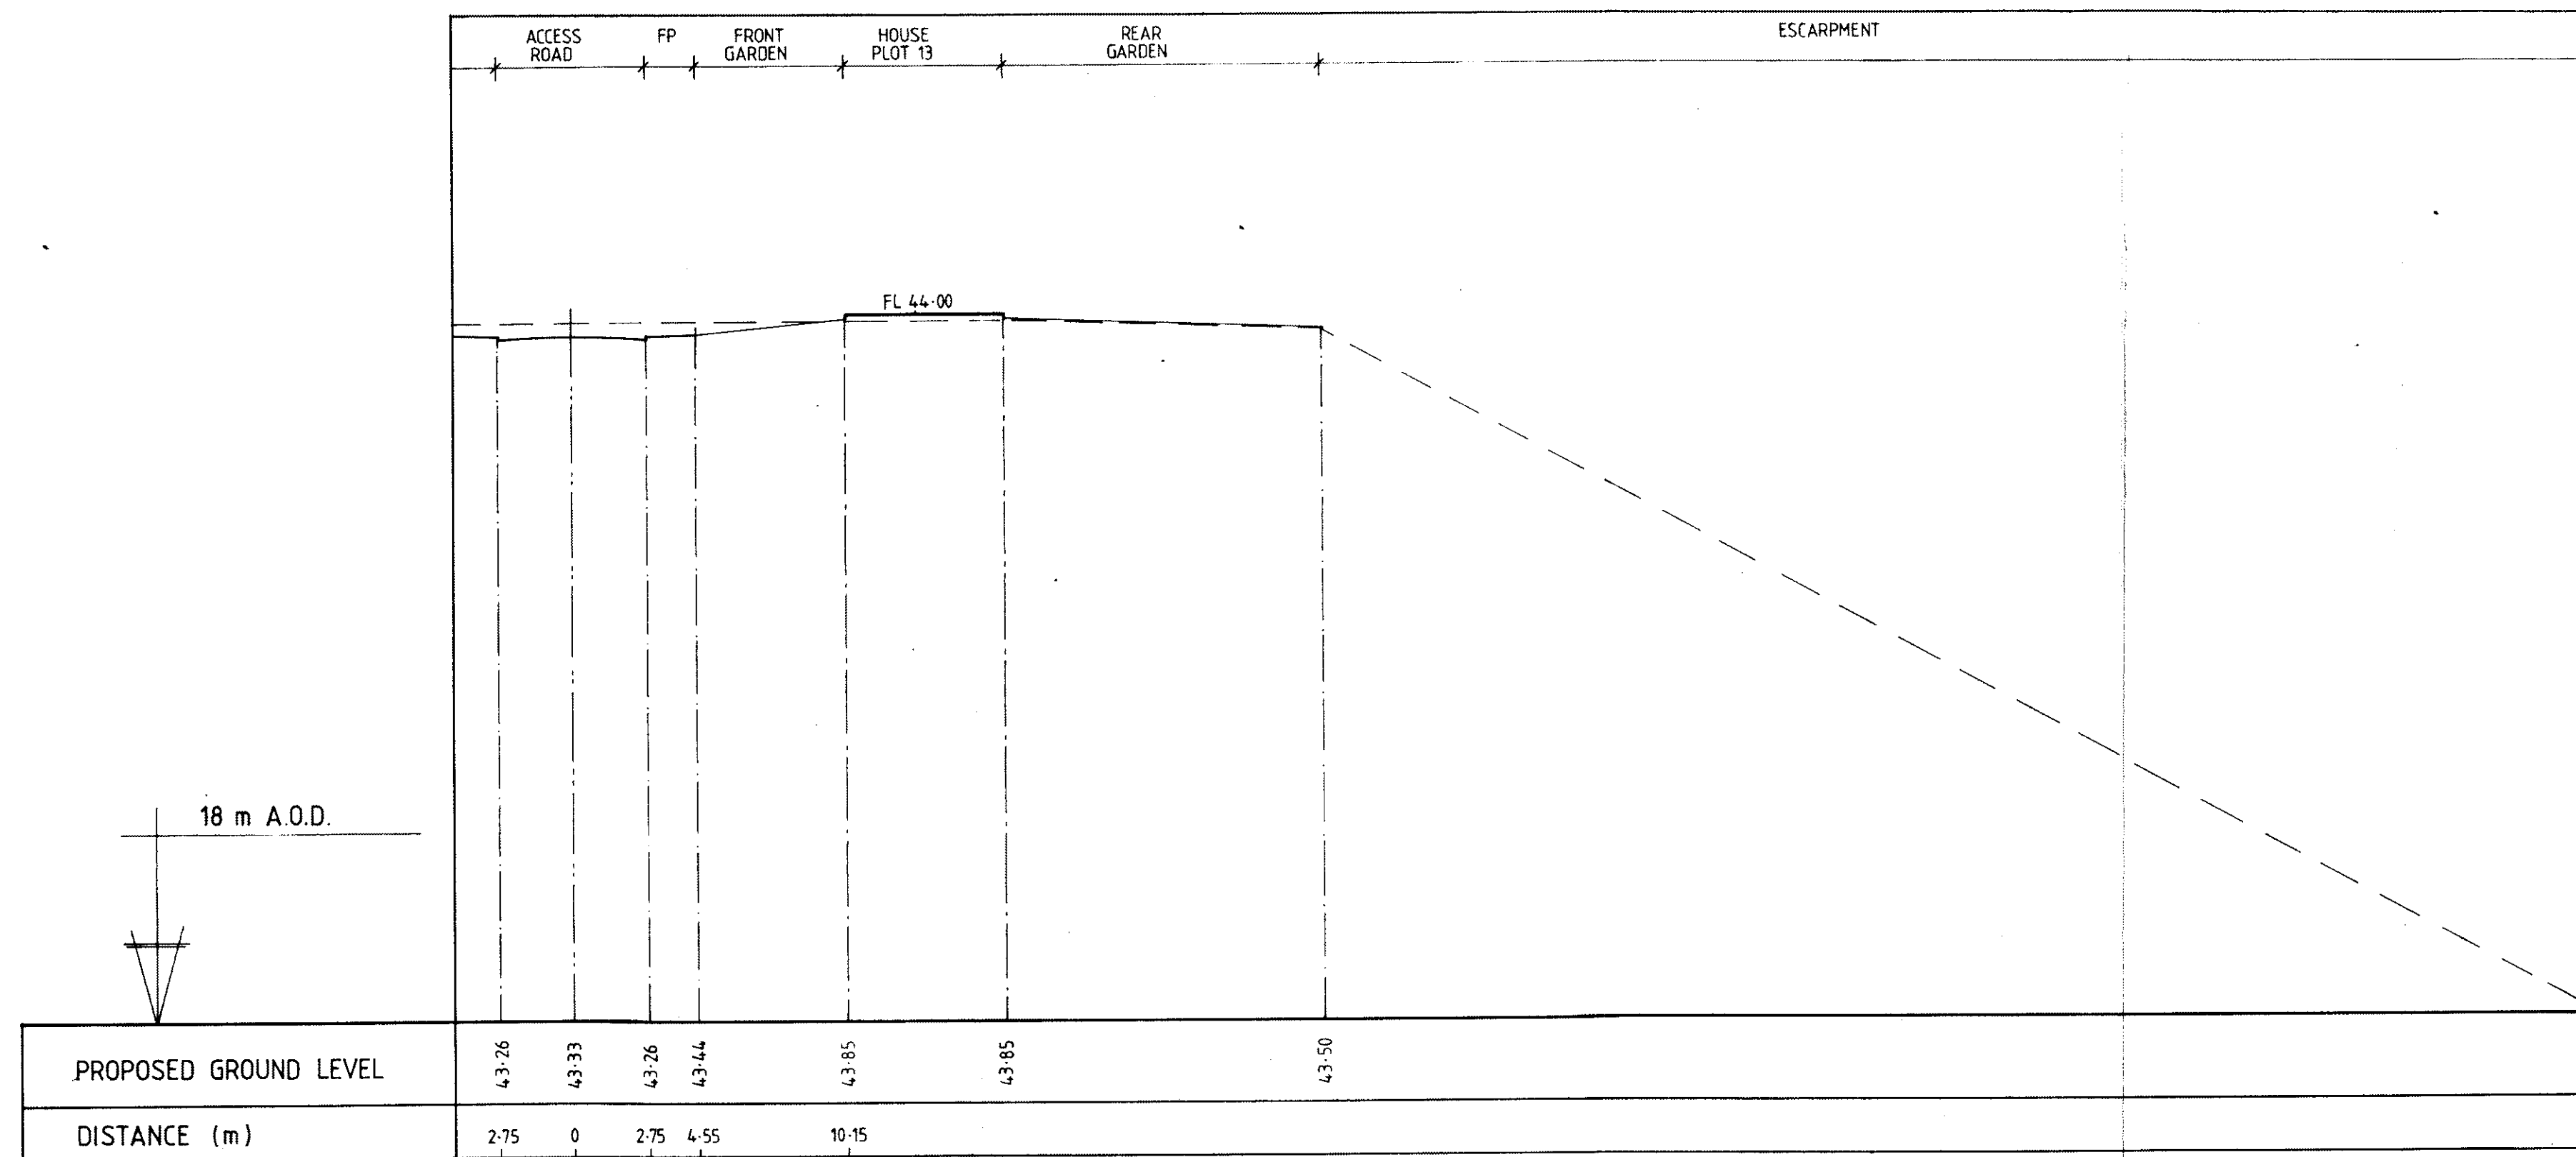

SECTION 6.

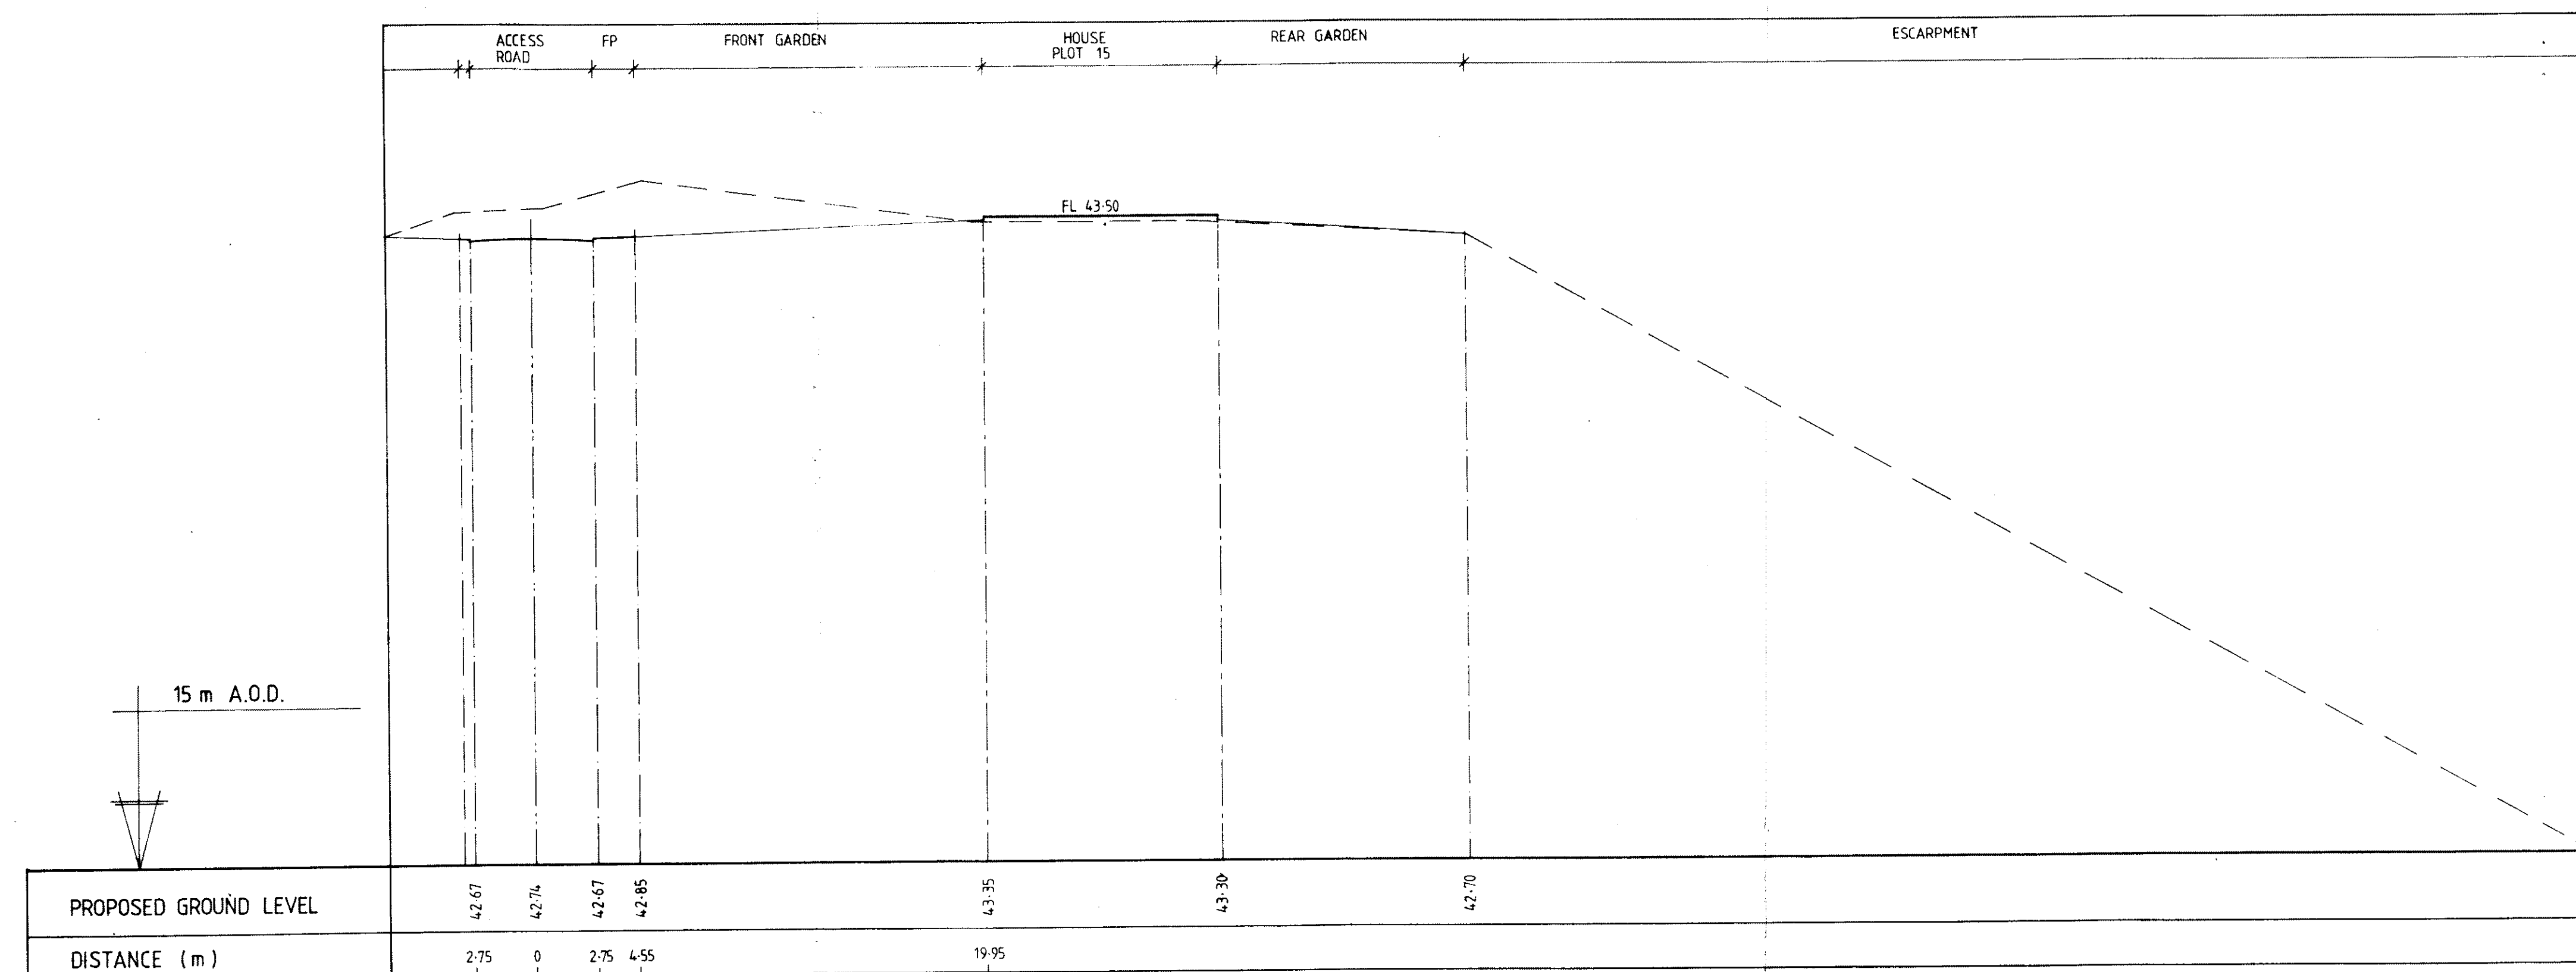

NOTES:
All dimensions must be checked on site and not scaled from this drawing

A	Date	Revisions

© copyright

Client

Job Title

GREAT HOUSE FARM, LLANDOUGH,
PENARTH.


Drawing Title



ACCESS ROAD AND HOUSE
CROSS SECTIONS.

Scale 1: 200

Date MAR '92 Drawn by N.R.

Drg.No. E 100/5 Rev.

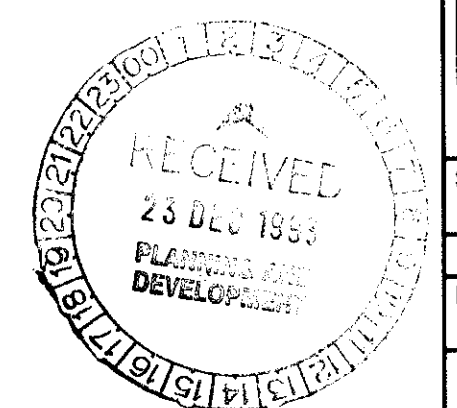

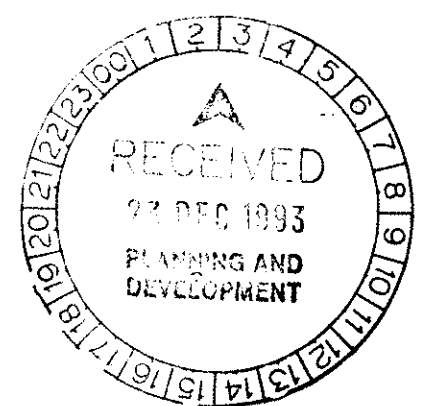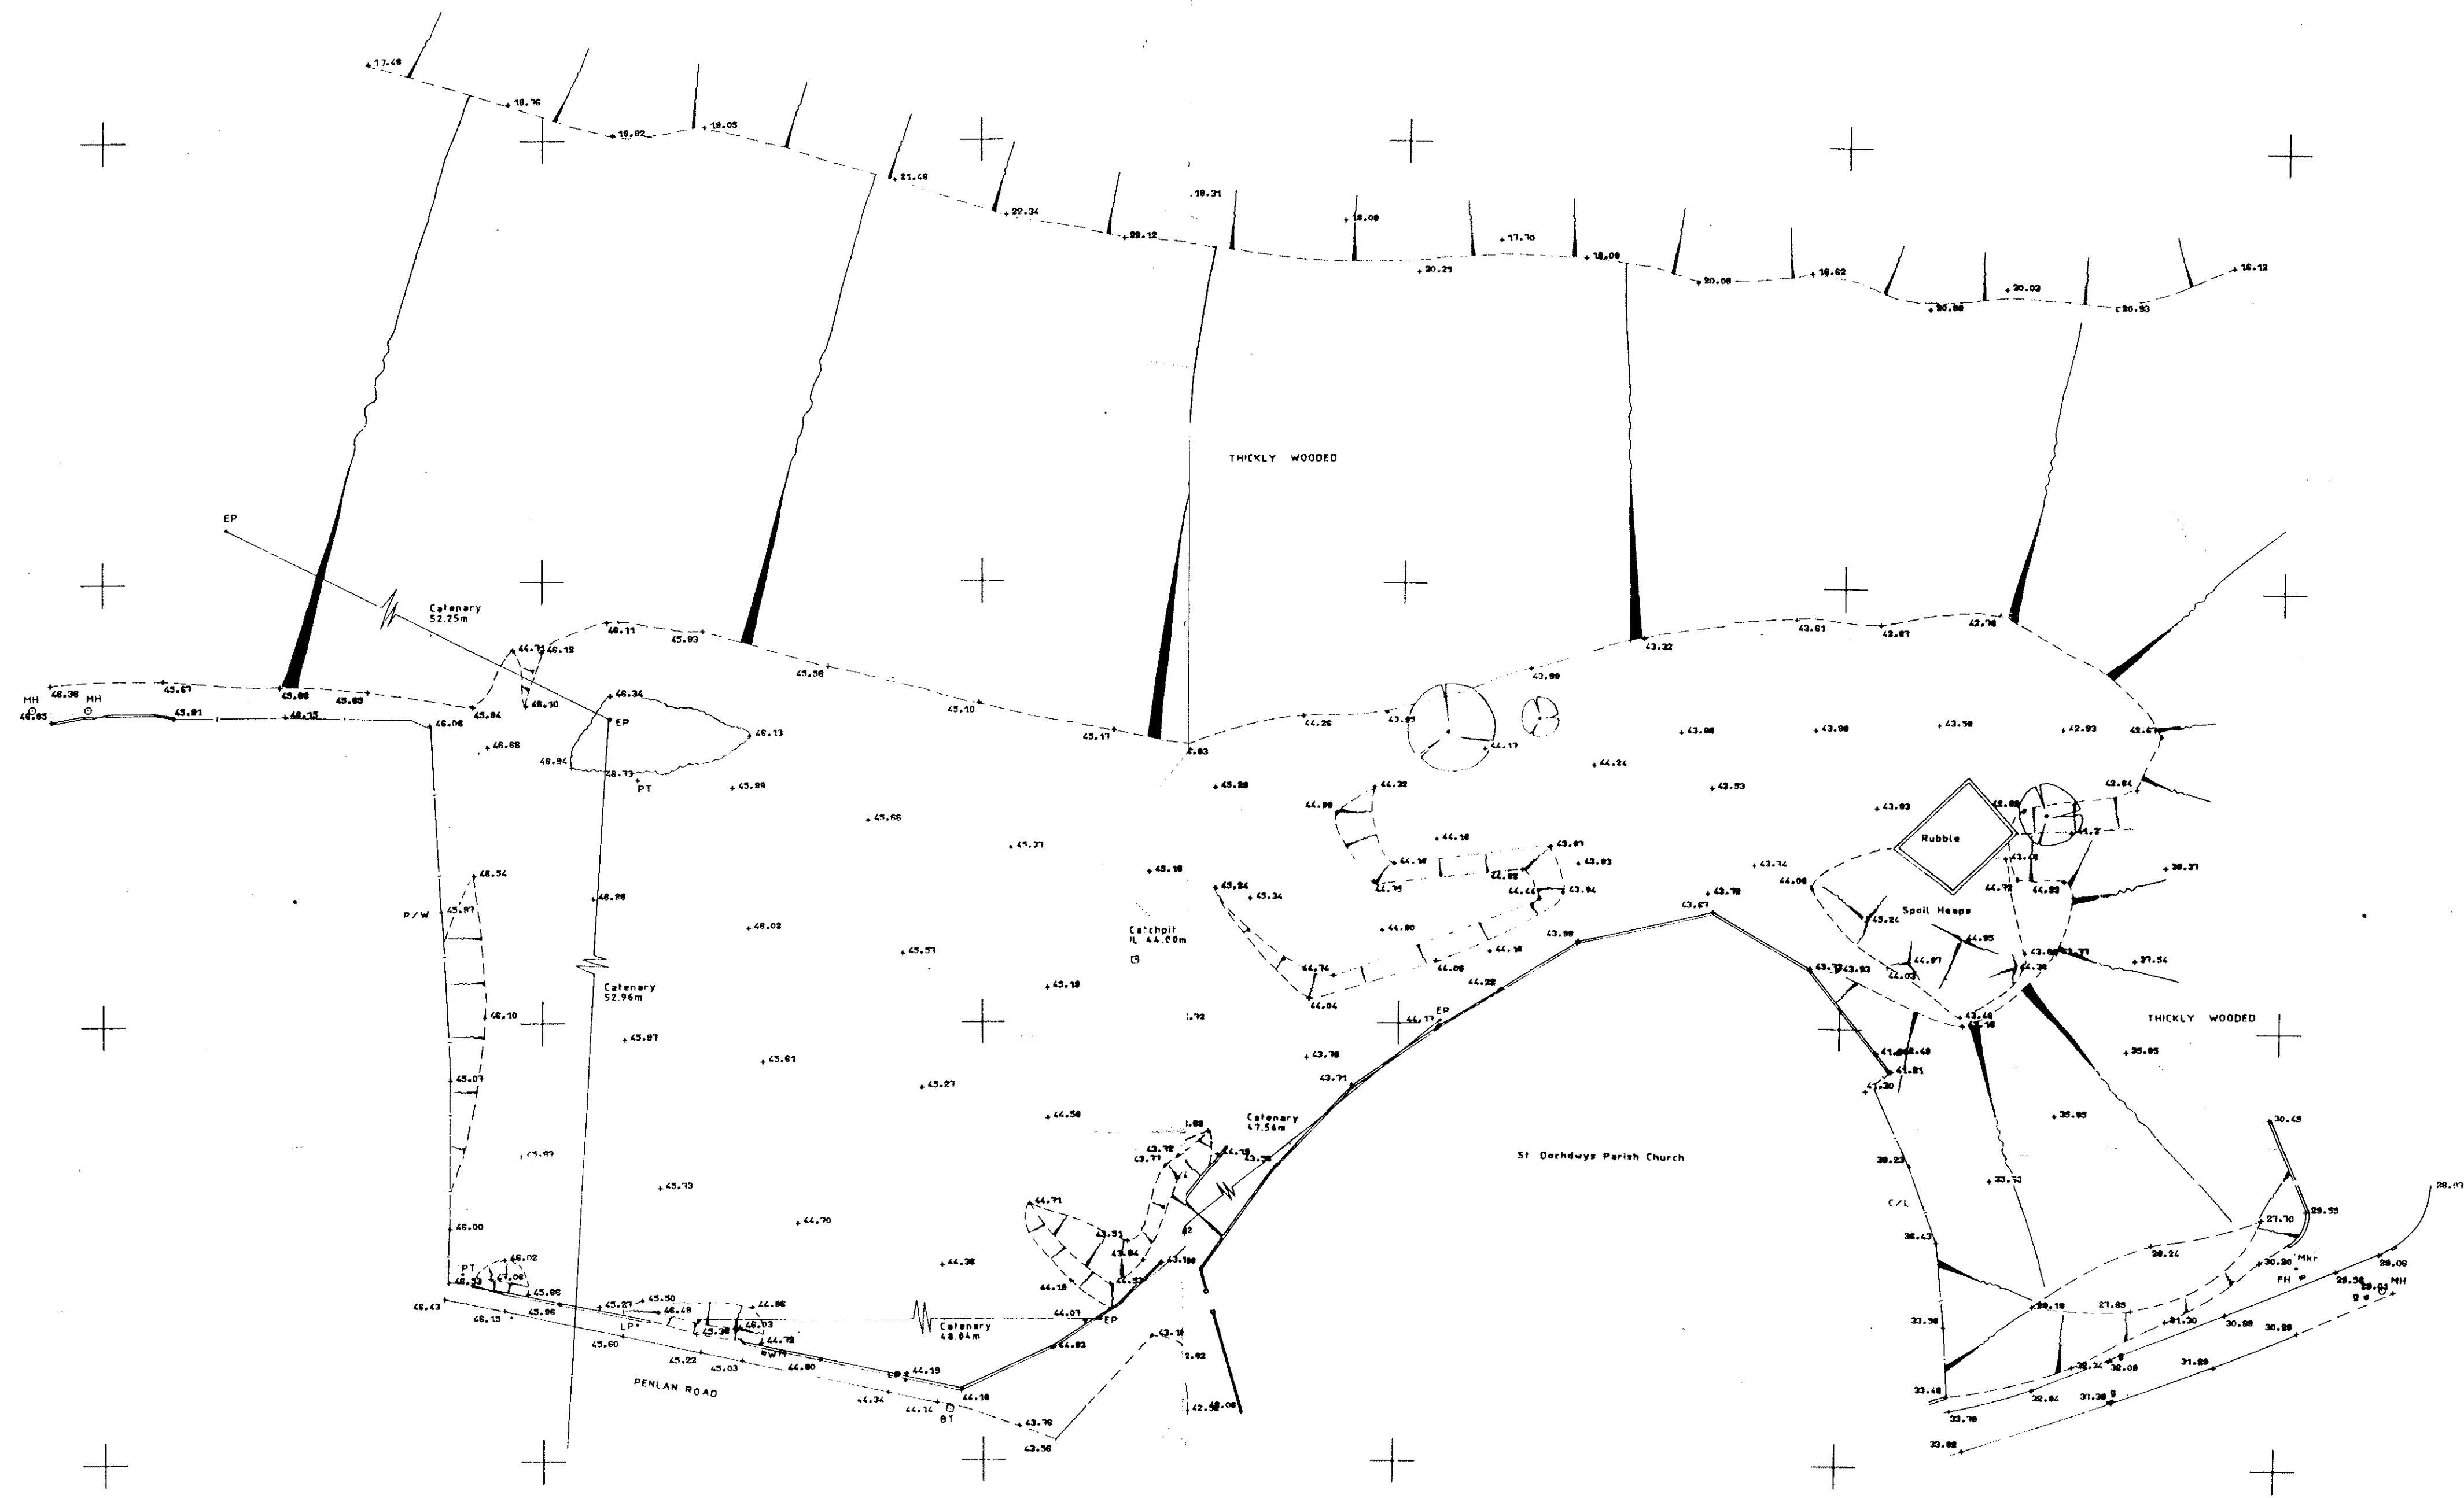

LLANDOVERY FARM LLANDUGH SITE SURVEY

LEVELS RELATED TO O.S.M. ON WALL OF
19 PENLAN ROAD = 42.35M A.O.D.

THIS DRAWING REMAINS THE PROPERTY OF JOHN R. JENKINS
UNTIL ALL FEES ARE PAID IN FULL

HUBERT JENKINS & PARTNERS
CONSULTING ENGINEERS
OCEAN BUILDINGS BUTE CRESCENT
CARDIFF CF1 6AN

SCALE 1/500

DATE MAY 1989

DRAWING

LAND SURVEYMENT ARICS
CONSULTING SURVEYOR
100A/11 NORTH ROAD
CARDIFF CF1 1NU TEL: (04463) 2109

DRAWING NO. 136/5/89