


OFFICE COPY



Llandough
(Llandochau)

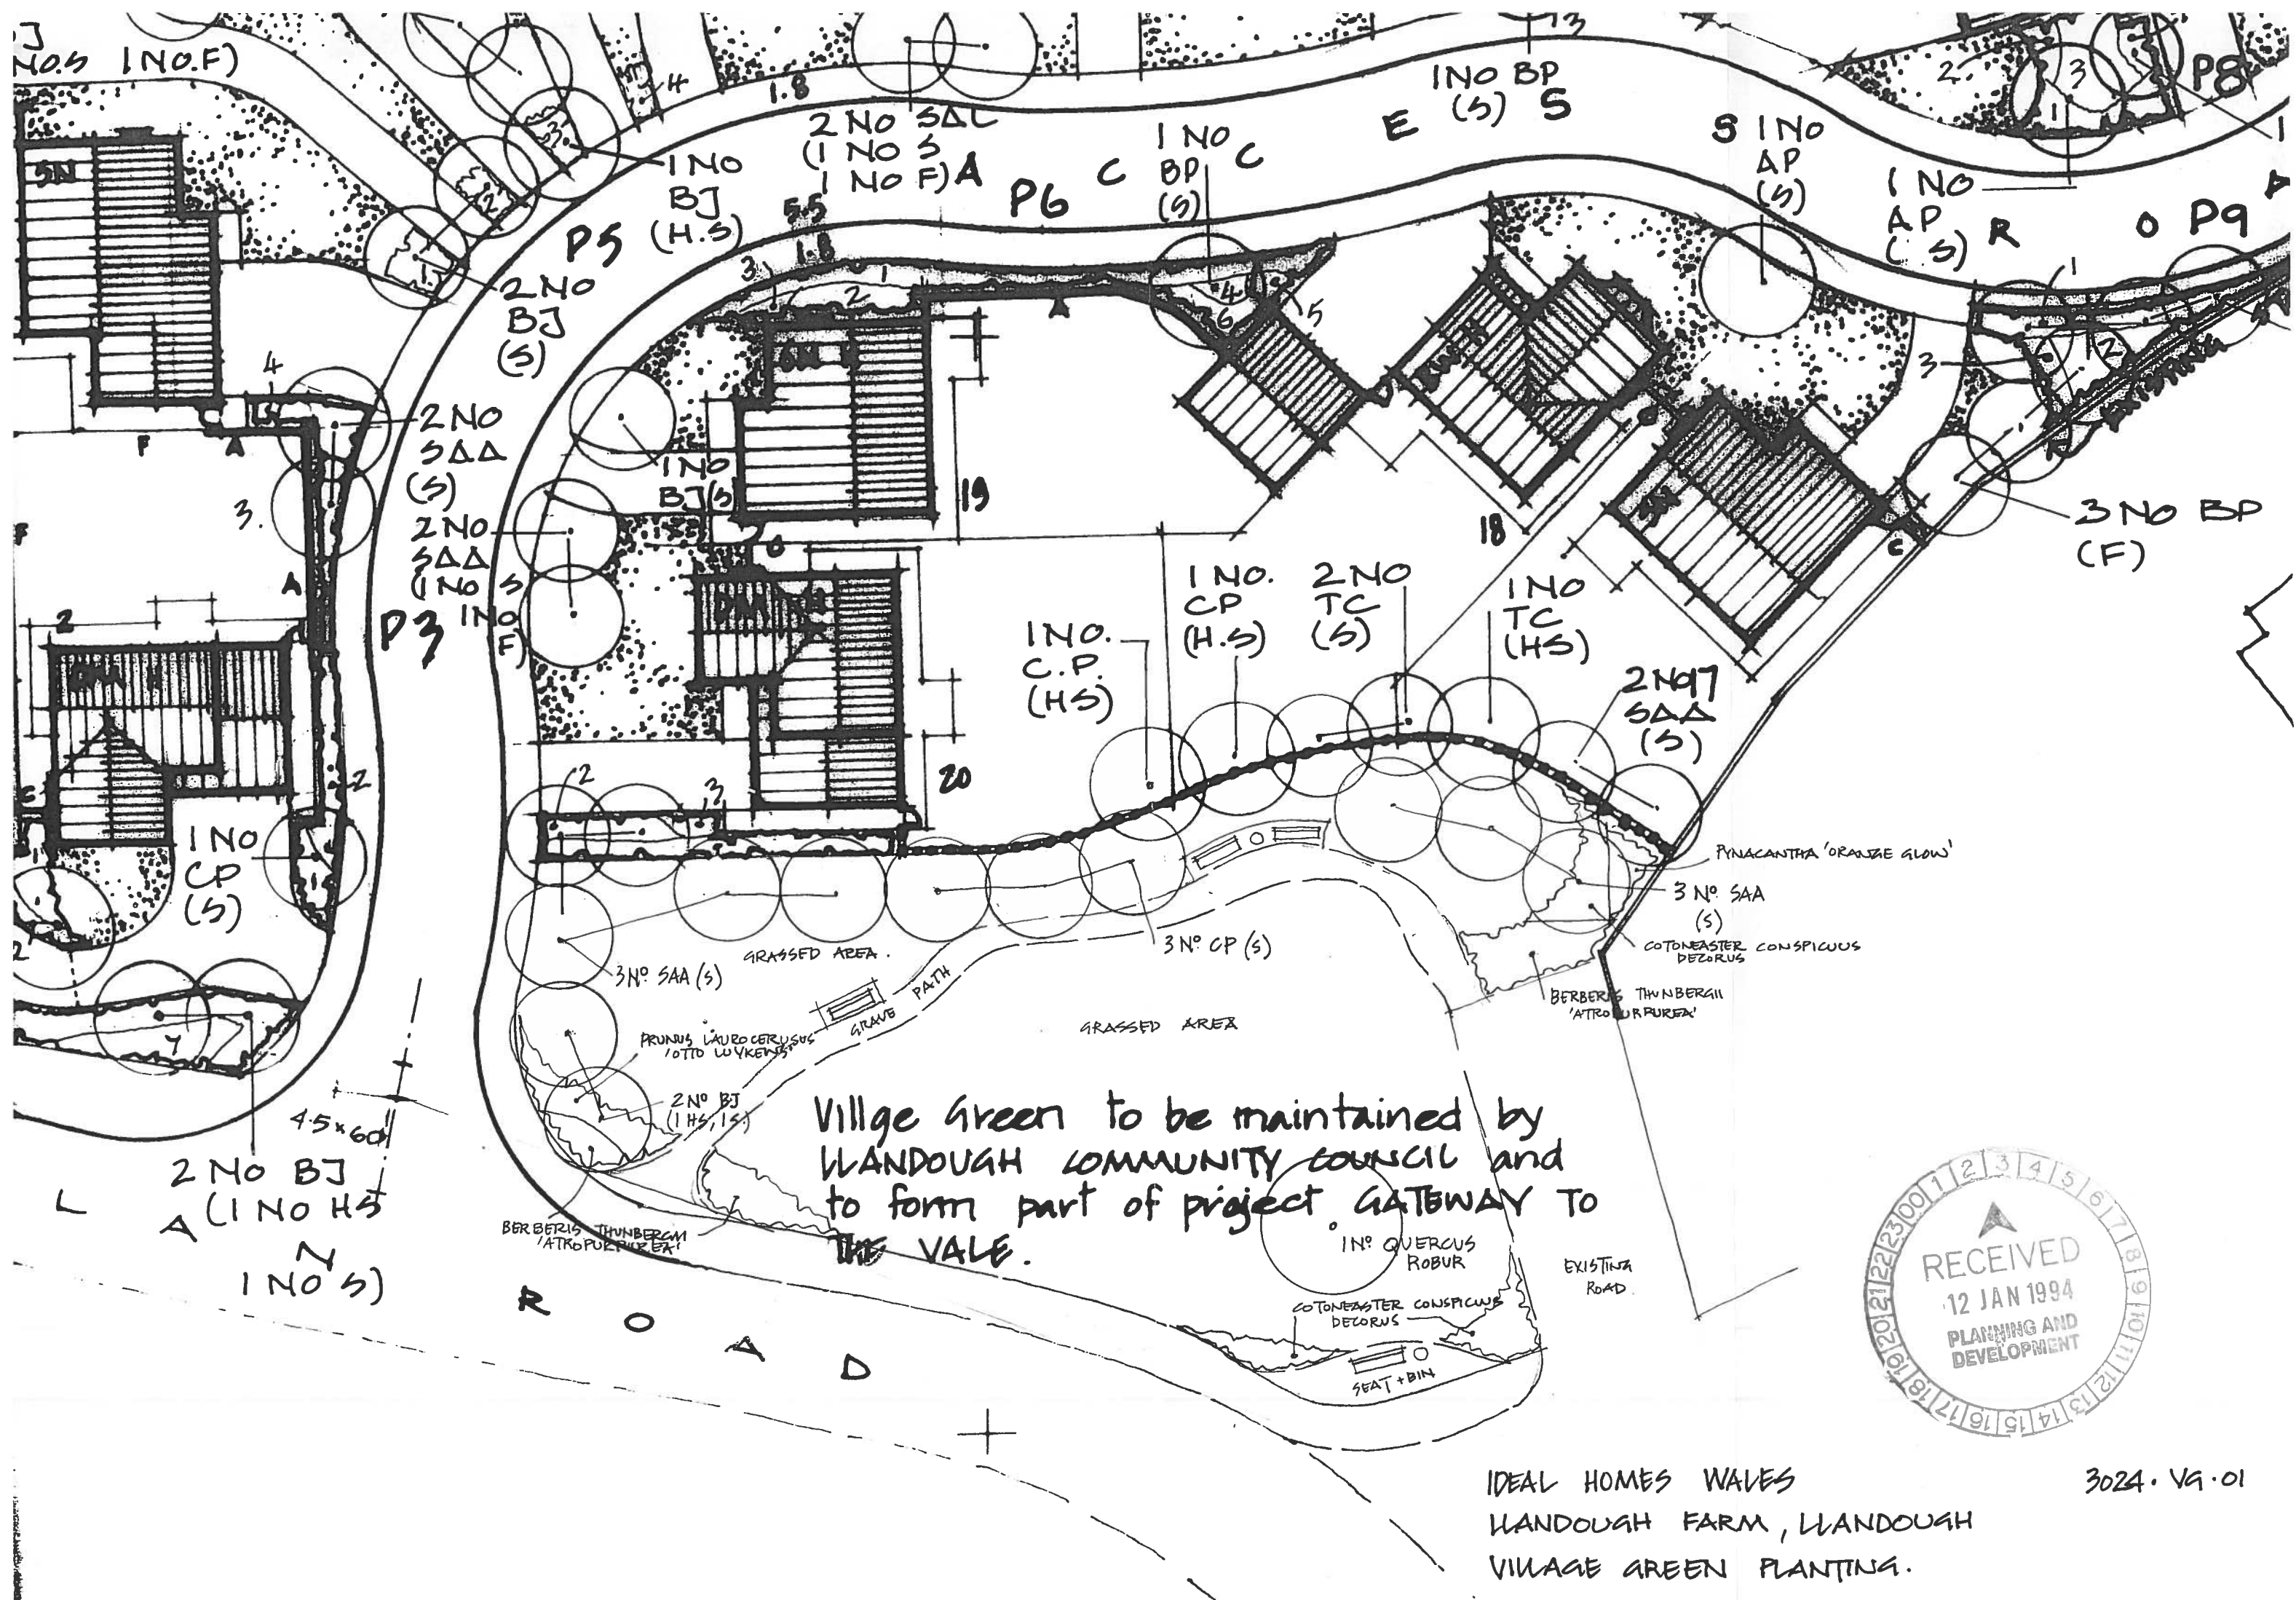

Area to be maintained by
FOREST OF CARDIFF GROUP.



1800 HIGH STONE WALL - OUT OF
EXISTING STONE WALLS TO BE
DEMOLISHED ALONG FRONTAGE

OPEN SPACE / GREEN

Village Green to be maintained by
LLANDOUGH COMMUNITY COUNCIL and
to form part of project GATEWAY TO
THE VALE.

- A 1800 HIGH FACING BRICK WALL WITH TILE COPING
- C 1800 HIGH CLOSE BOARDED TIMBER SCREEN
- F 900 HIGH PLASTIC COATED CHAIN LINK FENCE
- PEDESTRIAN GATE
- 900 WIDE FOOTPATH
- PROPOSED PLANTING
- TURF BY DEVELOPER
HANDLED PLAN.

HOUSE TYPES:

DM	DENHAM	6
SN	SUTTON	9
BW	BUDWORTH	5
		20




+ Ideal
Homes

REVISIONS		CLIENT IDEAL HOMES WALES JOB TITLE LLANDOUGH FARM, LLANDOUGH DRWG TITLE SITE LAYOUT.		Wyn Thomas+Partners 	
wn	Checked	Date MAR 92	Scale 1:500	Job 4	Dwg TP.100


DO NOT SCALE
Dimensions must be verified
by main contractor on site. If
in doubt refer to Architect.



FRONT ELEVATION

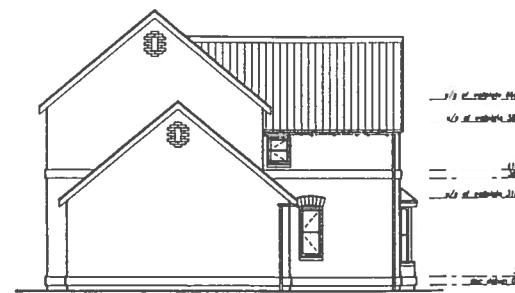

SIDE ELEVATION

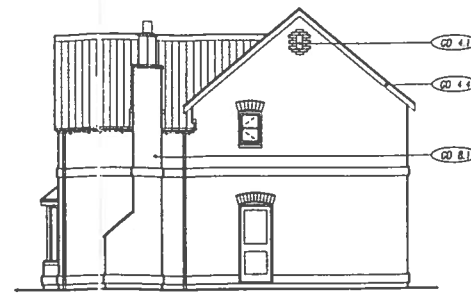

SIDE ELEVATION



REAR ELEVATION

DO NOT SCALE from this drawing
All dimensions must be verified at the site before setting out
commencing work or making any shop drawings.

ELECTRICAL LEGEND


Single way light switch	1.3amp socket outlet at high level
2 way light switch	Cooker control panel with 1.3amp socket outlet @ high level
Intermediate light switch	Ball push
Pull cord	Door bell
Ceiling light point	3kw immersion heater
Mid light	Thermostat
Recessed down lighter	Central heating clock
Up lighter	TV Television aerial outlet
Shower point @ high level	FM radio aerial outlet
Light/shower point @ high level	Gas point
1.3amp switch socket outlet	Telephone outlet
1.3amp fused switched spur and neon light @ high level	British Telecom intake
1.3amp fused switched spur with neon light @ high level and flex outlet plate @ low level	Consumer control unit
1.3amp socket outlet	

9200671/RES


N.B.
• Denotes that dimensions are indicative and are to be adjusted to brick dimensions according to external wall thickness and relationship to adjoining properties

All windows to be recessed from brickwork face by 85mm. All windows to be double glazed.
All windows in kitchen and habitable room to have ventilation opening with a total area of 4000 sq mm. See detail sheets.

Kitchen extract fan to be set at 60 litres/sec or 30 litres/sec if incorporated in cooker hood.
Bedroom extract fan to be set at 15 litres/sec for intermittent operation.

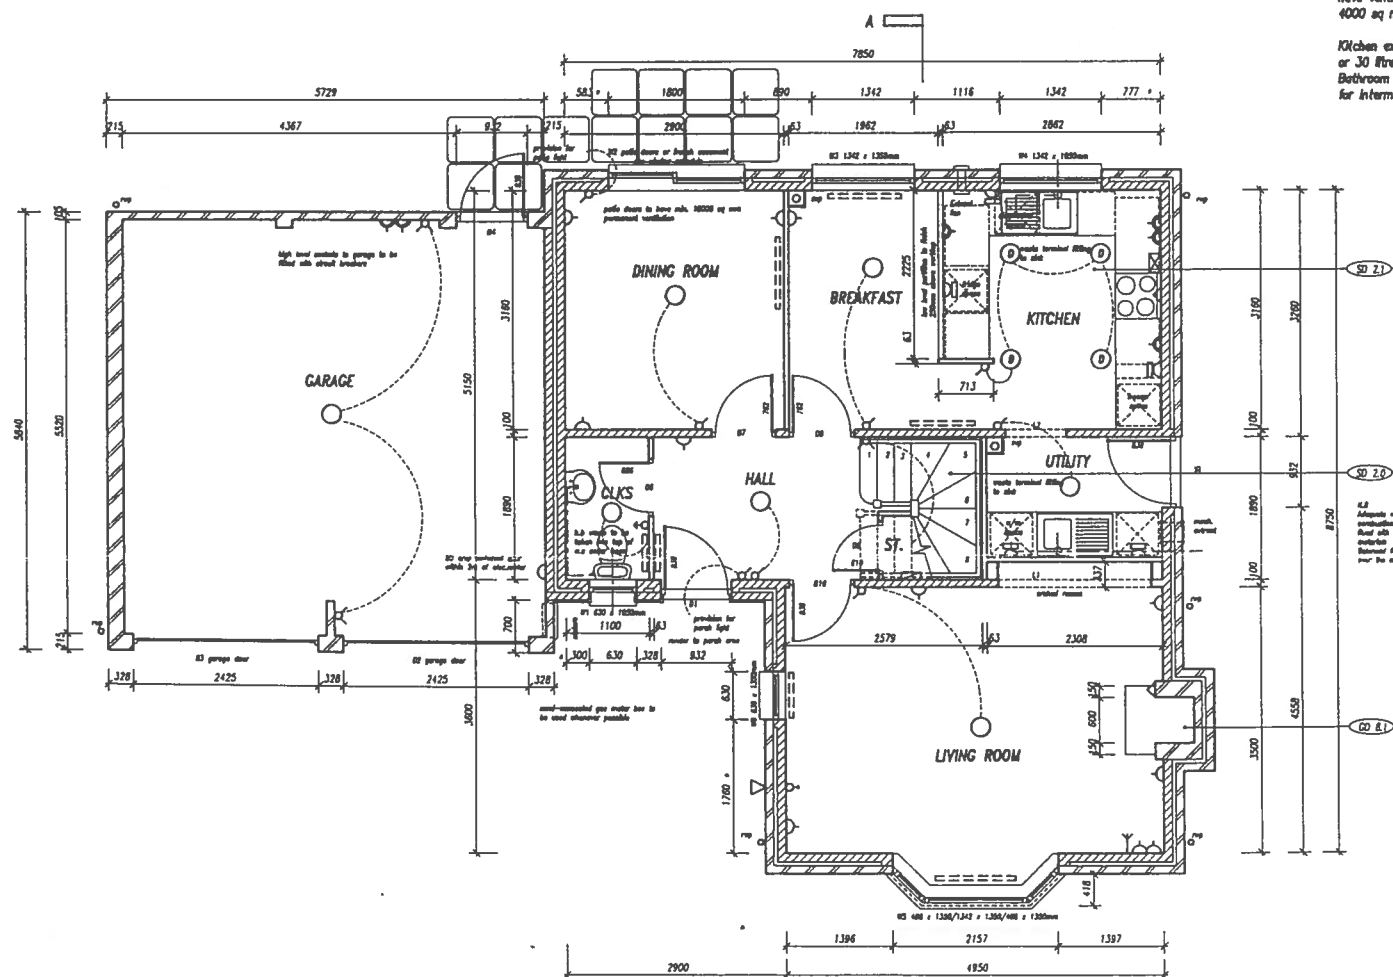

GROUND FLOOR PLAN

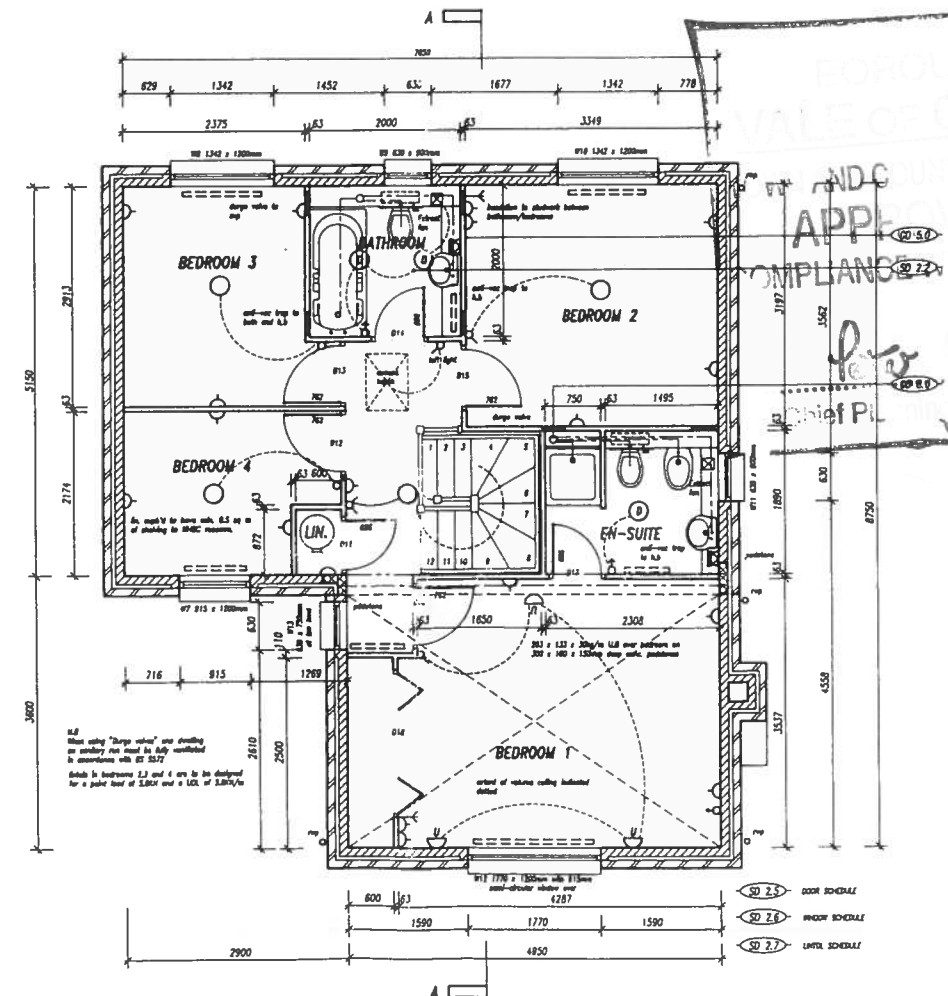

FIRST FLOOR PLAN

REV	DESCRIPTION	DATE
A	Rev's moved away from front elevation. Garage depth reduced to standard size. Bath and position sites added. Projecting band course added above dpc. Solid arch added over bedroom 1 window.	22.07.91

CD0.0 - GENERAL DETAILS
SD0.0 - SPECIFIC DETAILS

ideal
Homes

SITE
THE VILLAGE COLLECTION

THE BUDWORTH

TITLE
PLANS AND ELEVATIONS

SCALE
1:50 1:100

DATE
05.04.91

NUMBER
4H.117.1V/1.0

REVISION
A



* Denotes that dimensions are indicative and are to be adjusted to brick dimensions according to external wall thickness and relationship to adjoining properties

All windows to be recessed from brickwork face by 85mm. All windows to be double glazed. All windows in kitchens and habitable room to have ventilation opening with a total area of 4000 sq mm. See detail sheets.

Kitchen extract fan to be set at 60 litres/sec or 30 litres/sec if incorporated in cooker hood
Bathroom extract fan to be set at 15 litres/sec for intermittent operation.



DO NOT SCALE from this drawing

ELECTRICAL LEGEND

- | | | | |
|---|--|---|---|
|  | Single way light switch |  | 13amp socket outlet at high level |
|  | 2 way light switch |  | Cooker control panel with 13amp socket outlet at high level |
|  | Intermediate light switch |  | Bell push |
|  | Pull cord |  | Door bell |
|  | Ceiling light point |  | Jew immersion heater |
|  | Wall light |  | Thermostat |
|  | Recessed down lighter |  | Control heating clock |
|  | Up lighter |  | TV Television aerial outlet |
|  | Shower point @ high level |  | R FM radio aerial outlet |
|  | Light/shower point @ high level |  | Gas point |
|  | 13amp switch socket outlet |  | Telephone outlet |
|  | 13amp fused switched spur and neon light @ high level |  | British Telecom intake |
|  | 13amp fused switched spur with neon light @ high level and flex outlet plate @ low level |  | Consumer control unit |
|  | 13amp socket outlet | | |

REV	DESCRIPTION	DATE
A	Drp. number revised.	14.05.91
B	Parch area re-designed. Partition between living room and hall removed. Door to store moved to kitchen. Door to kitchen removed. Arch between living/dining increased to 1500mm. Utility reduced to 1500mm. Pwp's moved away from front elev. Beam and poststone sizes added. Projecting band course added over door. Drp. number revised due to change in floor area.	07.08.91
C	Original house type deleted and redrawn as a variation on the Milton.	20.08.91
D	Double garage option added.	19.09.91

BOROUGH OF THE
VALE OF GLAMORGAN
TOWN AND COUNTRY PLANNING ACT, 1990
APPROVED SUBJECT TO
COMPLIANCE WITH CONDITIONS IF ANY
- 3 SEP 1992
Taylor
Chief Planning and Development Officer

600.0 — GENERAL DETAILS
 500.0 — SPECIFIC DETAILS

**Ideal
Homes**

SITE _____
THE VILLAGE COLLECTION

THE SUTTON

PLANS AND ELEVATIONS

SCALE


1:50 1:100
— NUMBER —
4H.119.2V/1.0

DATE 23.04.91

REVISION



FRONT ELEVATION

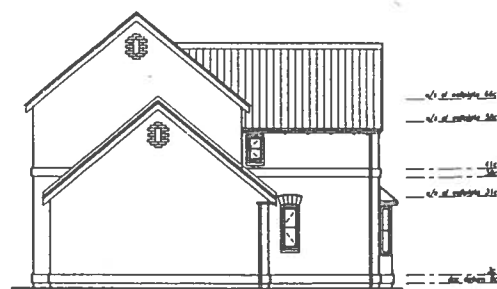

SIDE ELEVATION



SIDE ELEVATION



REAR ELEVATION


92/0067 1/RES

DO NOT SCALE from this drawing
All dimensions must be verified at the site before setting out
commencing work or making any shop drawings.

ELECTRICAL LEGEND

- | | |
|---|---|
| Single way light switch | 1.5amp socket outlet at high level |
| 2 way light switch | Cooker control panel with 1.5amp socket outlet @ high level |
| Intermediate light switch | Bell push |
| Pull cord | Door bell |
| Ceiling light point | 3.6 immersion heater |
| Wall light | Thermostat |
| Recessed down lighter | Central heating clock |
| Up lighter | TV Television aerial outlet |
| Shower point @ high level | FM radio aerial outlet |
| Light/shower point @ high level | Gas point |
| 1.5amp switch socket outlet | Telephone outlet |
| 1.5amp fused switched spur and neon light @ high level | British Telecom intake |
| 1.5amp fused switched spur with neon light @ high level and flex outlet plate @ low level | Consumer control unit |
| 1.5amp socket outlet | |

REV	DESCRIPTION	DATE
A	Window ref. 100 revised. Dry number revised.	14.05.91
B	Prop's moved away from front elevation. Garage reduced to standard length. Beam and positions altered added. Projecting band course added above dpc. Solidus arch added over bedroom 1 window.	18.07.91

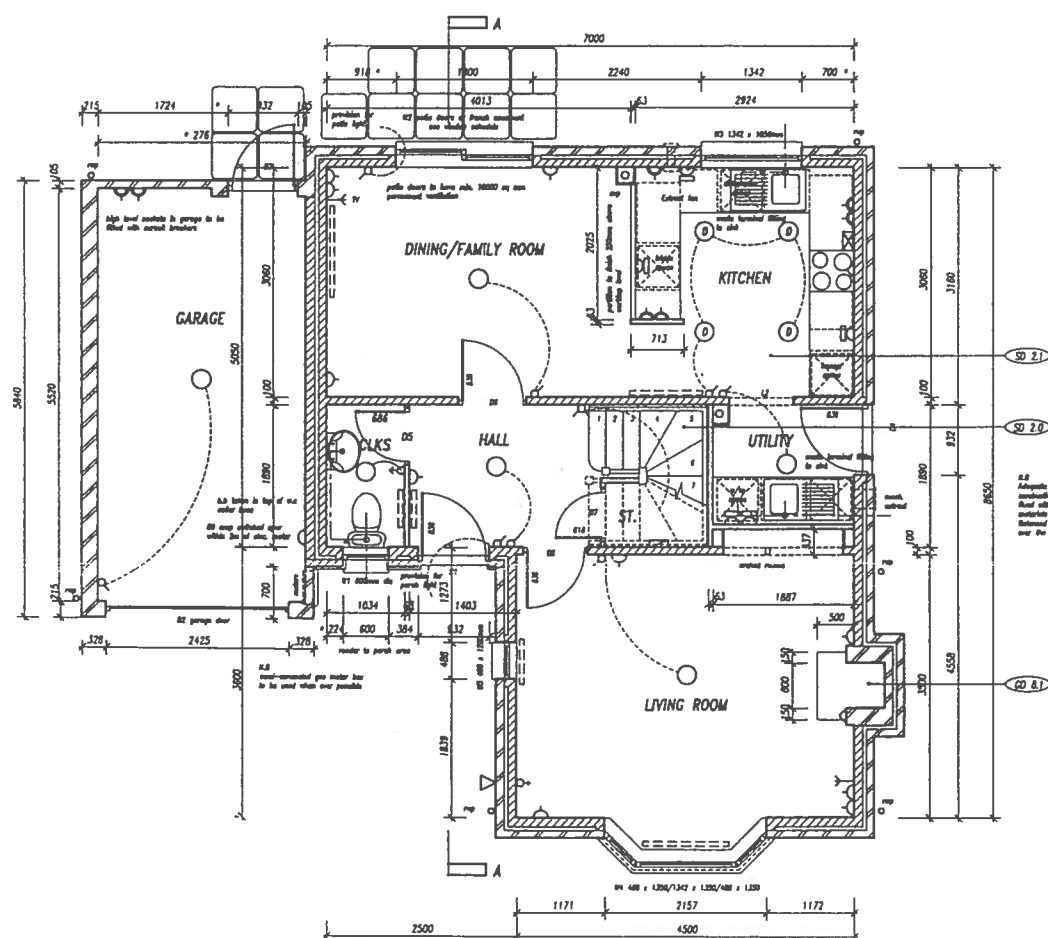


GROUND FLOOR PLAN

N.B.
• Denotes that dimensions are indicative and are to be adjusted to brick dimensions according to external wall thickness and relationship to adjoining properties.


All windows to be recessed from brickwork face by 65mm. All windows to be double glazed. All windows in kitchens and habitable room to have ventilation opening with a total area of 4000 sq. mm. See detail sheets.

Kitchen extract fan to be set at 60 litres/sec or 30 litres/sec if incorporated in cooker hood. Bathroom extract fan to be set at 15 litres/sec for intermittent operation.

N.B.
Adequate ventilation to be provided for circulation air to be kept at 15 litres/sec. All windows to be double glazed. All windows in kitchens and habitable room to have ventilation opening with a total area of 4000 sq. mm. See detail sheets.

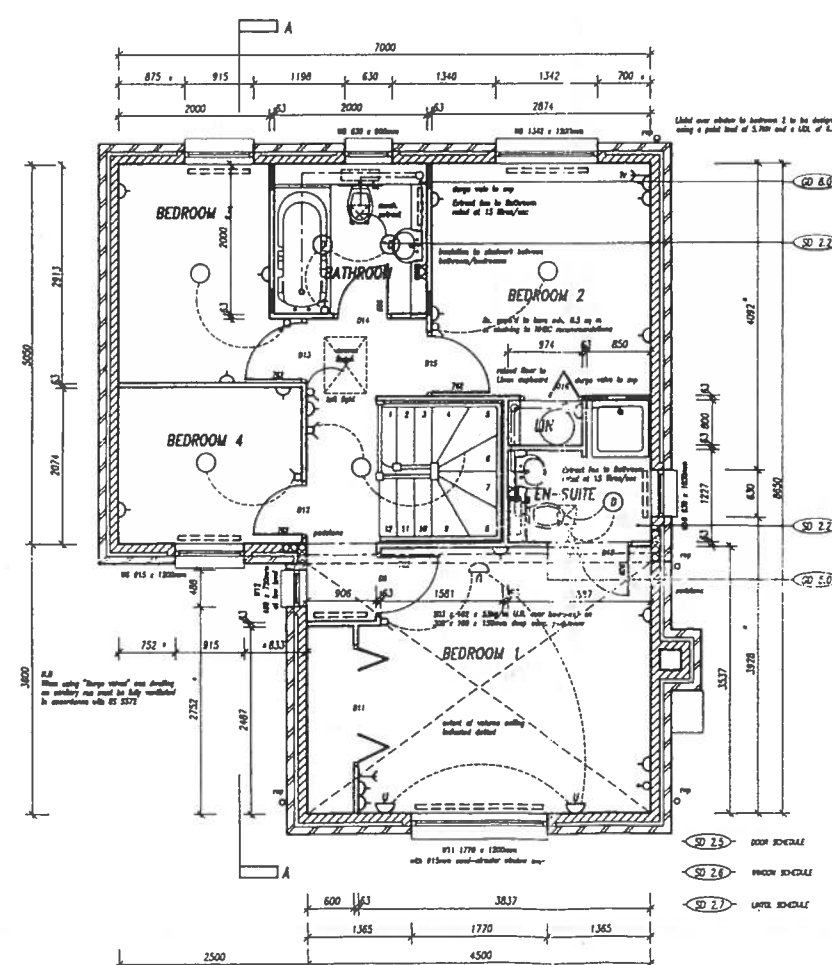

FIRST FLOOR PLAN

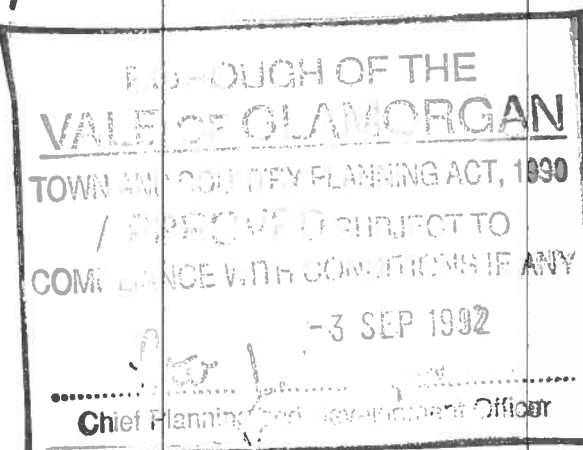

000.0 = GENERAL DETAILS
000.0 = SPECIFIC DETAILS

Ideal Homes

SITE
THE VILLAGE COLLECTION

THE DENHAM

TITLE
PLANS AND ELEVATIONS

SCALE
1:50 1:100


DATE
02.04.91

NUMBER
4H.104.1V/1.0

REVISION
B


DO NOT SCALE from this drawing
All dimensions must be verified at the site before setting out :
commencing work : or making any shop drawings.

REV	DESCRIPTION	DATE
A	Projecting band course added above dpc	29.07.91


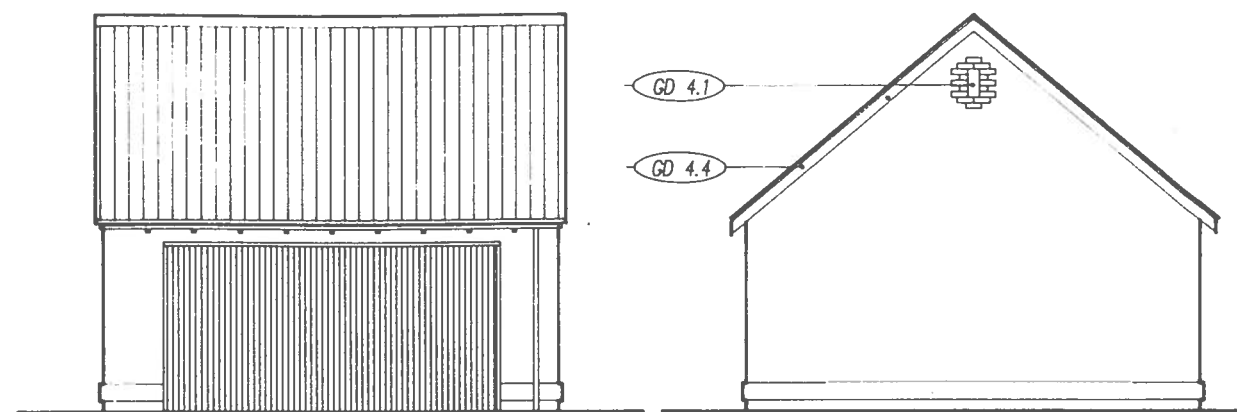


FRONT ELEVATION


SIDE ELEVATION

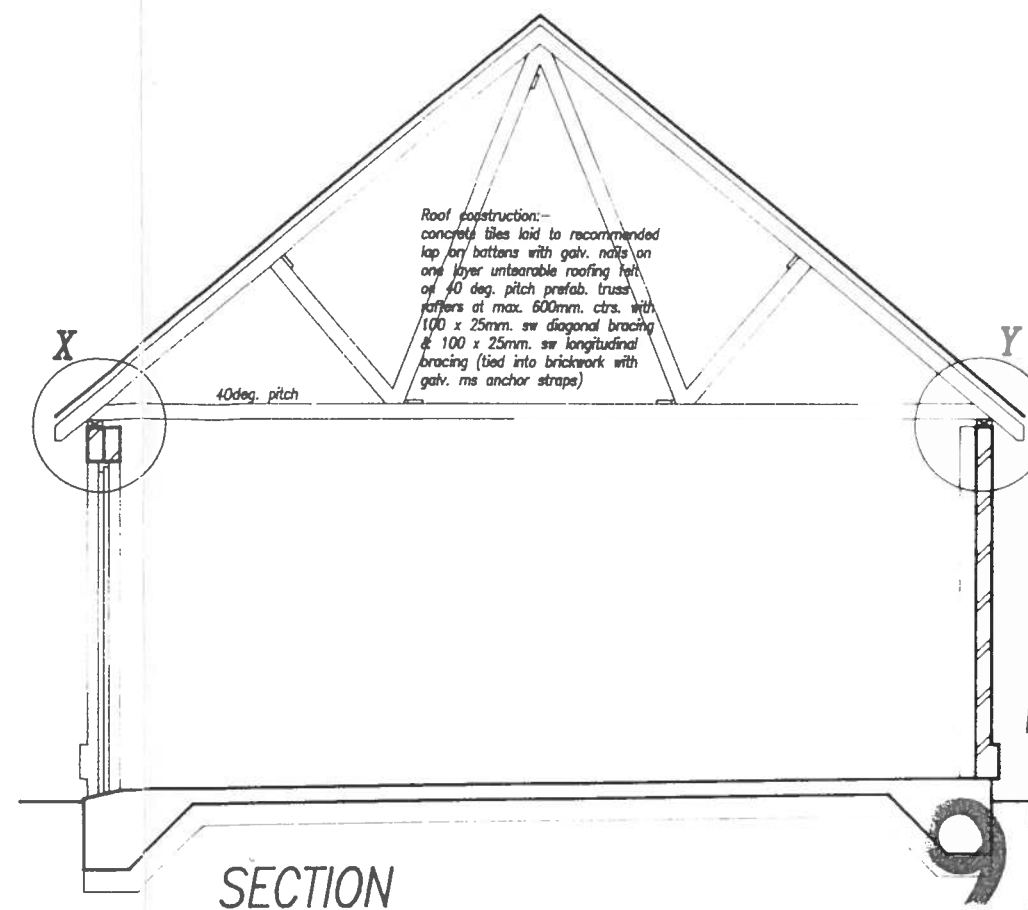


SECTION

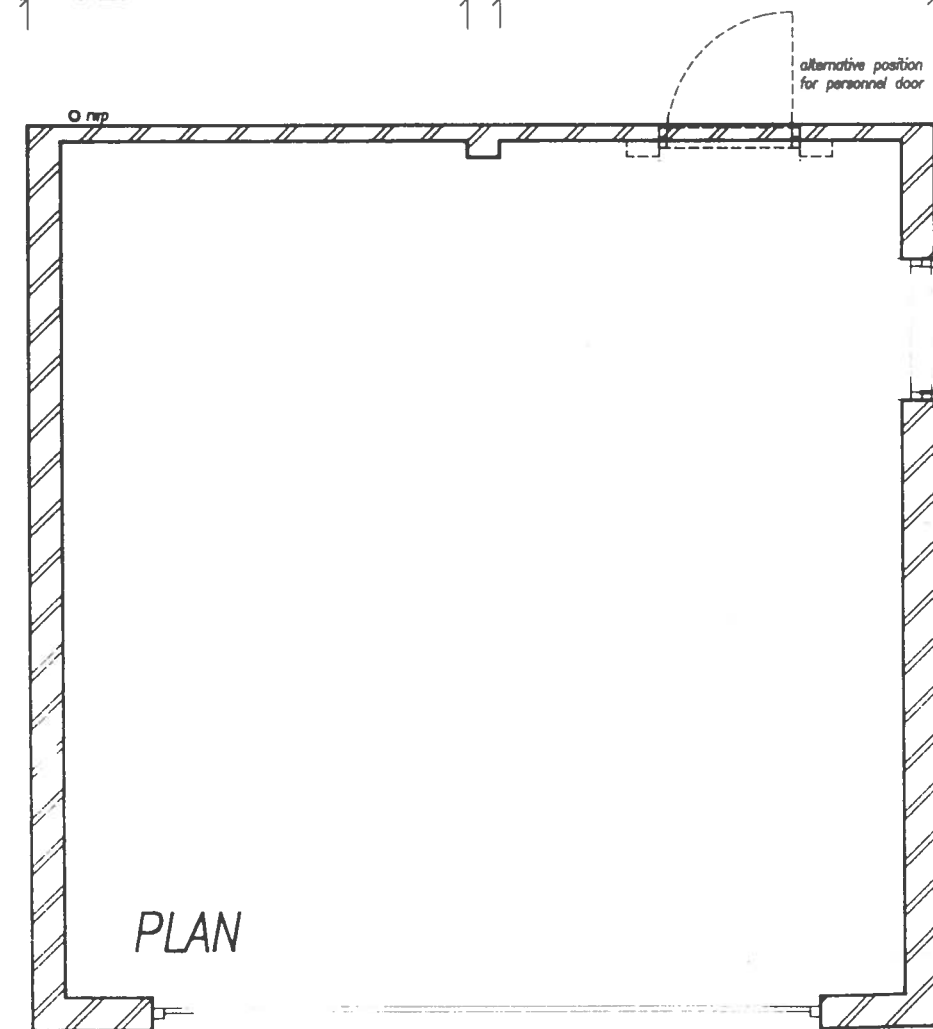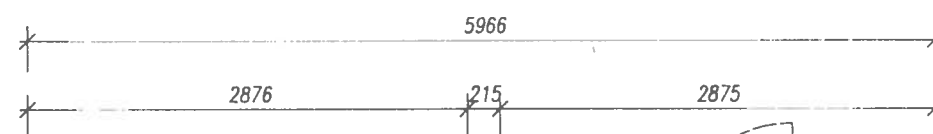

PLAN

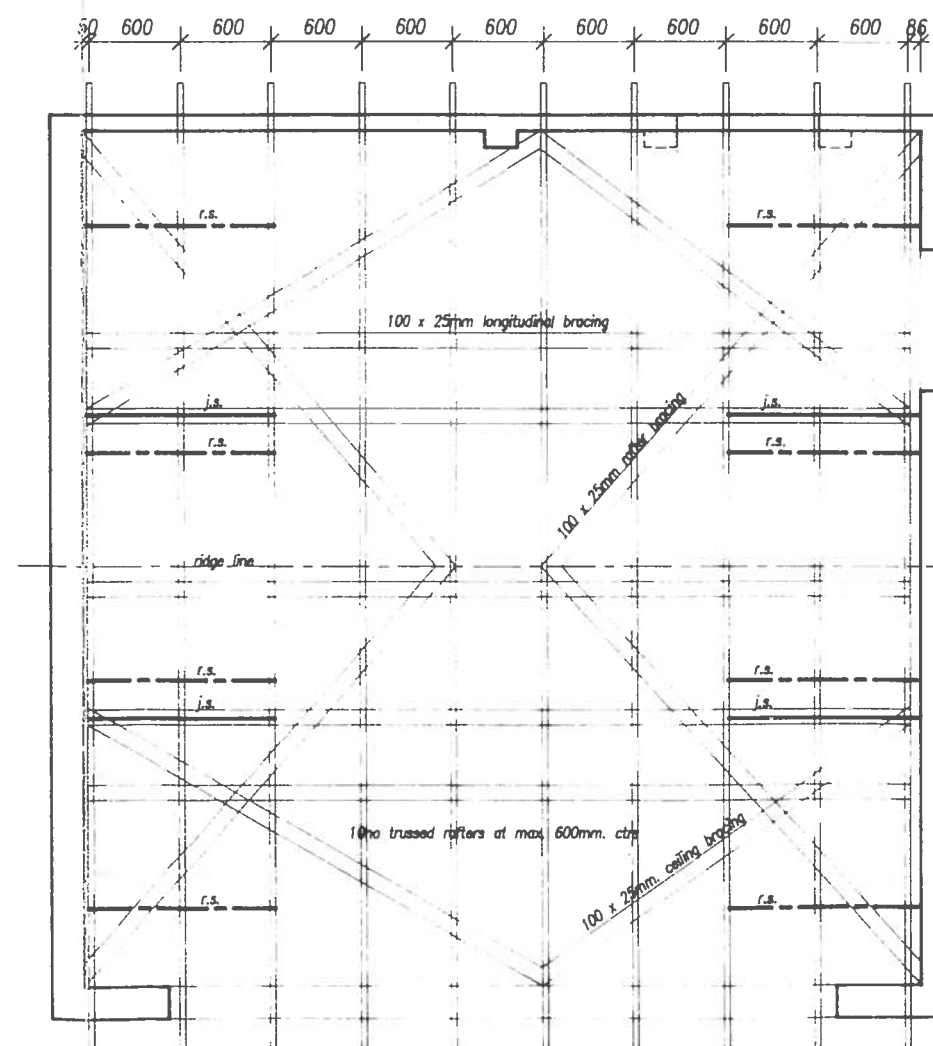

ROOF CARCCASING PLAN

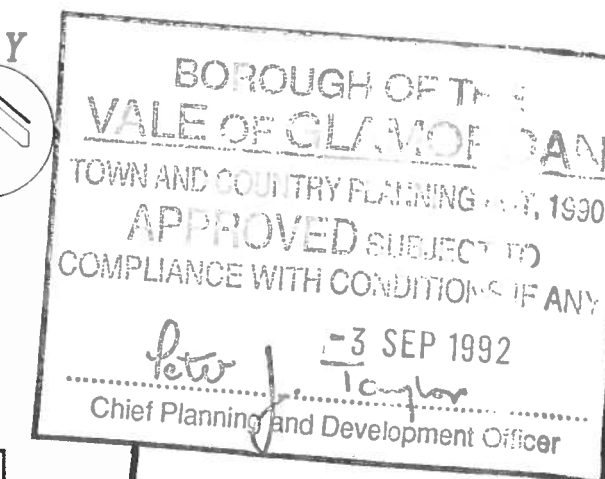

9200671/RES

- ROOF:
- All trusses shall be designed & fabricated to BS 5268 pt3 1985
 - All roof bracing shall be 100 x 25mm & shall be free from major strength reducing defects and distortion. They shall be fixed with 2no 3.35 x 75mm galv. round wire nails at every truss they cross
 - j.s = joist strap
 - r.s = rafter strap
 - Noggins to be provided to support m.s straps in all cases



GENERAL DETAIL

TITLE
GARAGE DETAILS
DETACHED GARAGE

SCALE
1:50 & 1:100


DATE
07.05.91

NUMBER
GD 8.2
SHEET No 2 OF 6


REV
A

PLOT AT 1-1


C.S.1

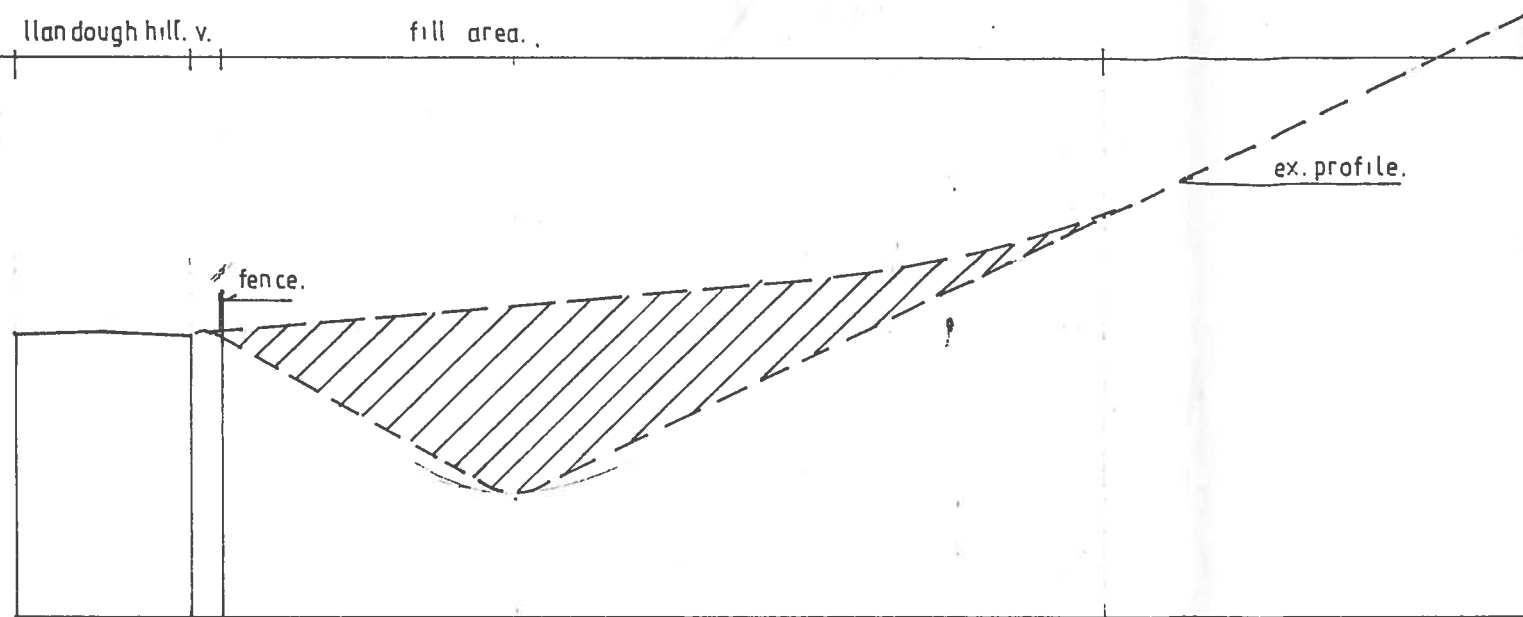

C.S.2

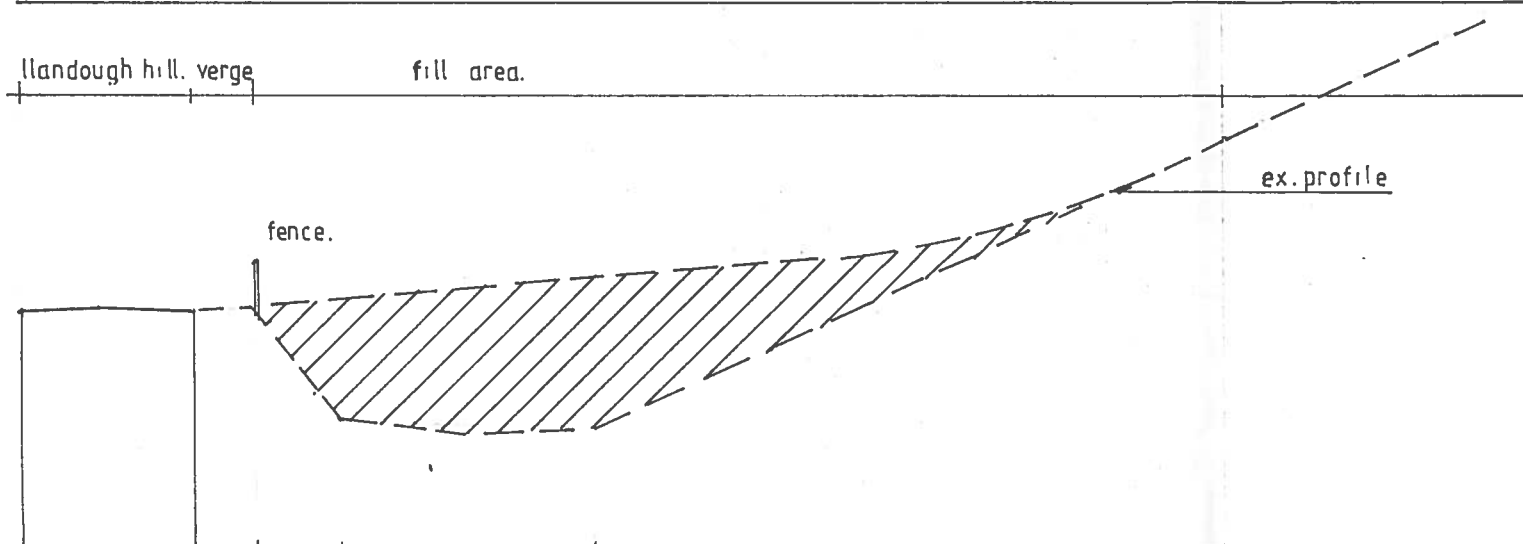

C.S.3

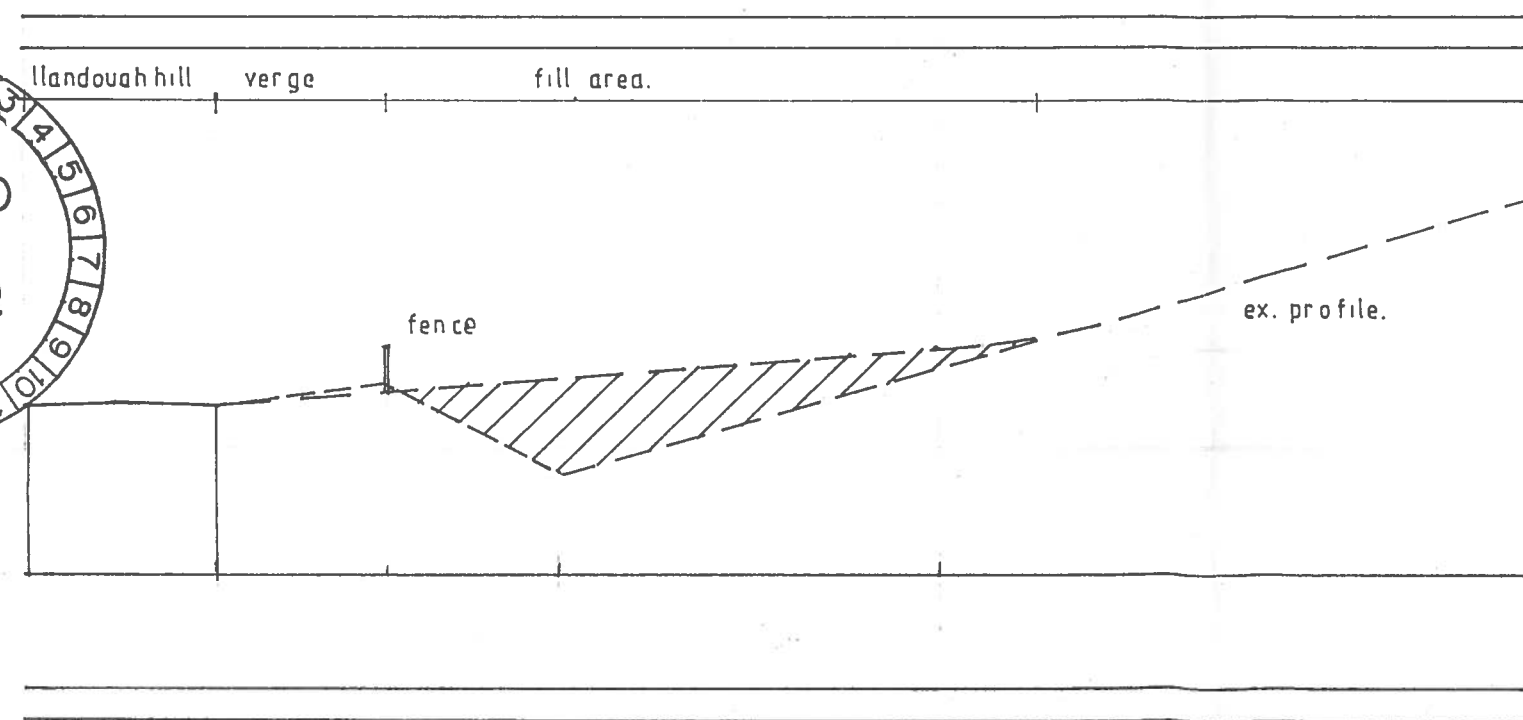


filling of existing depression.

scale: 1/200 natural.


llandough farm. llandough.

drwg no. E100./07.

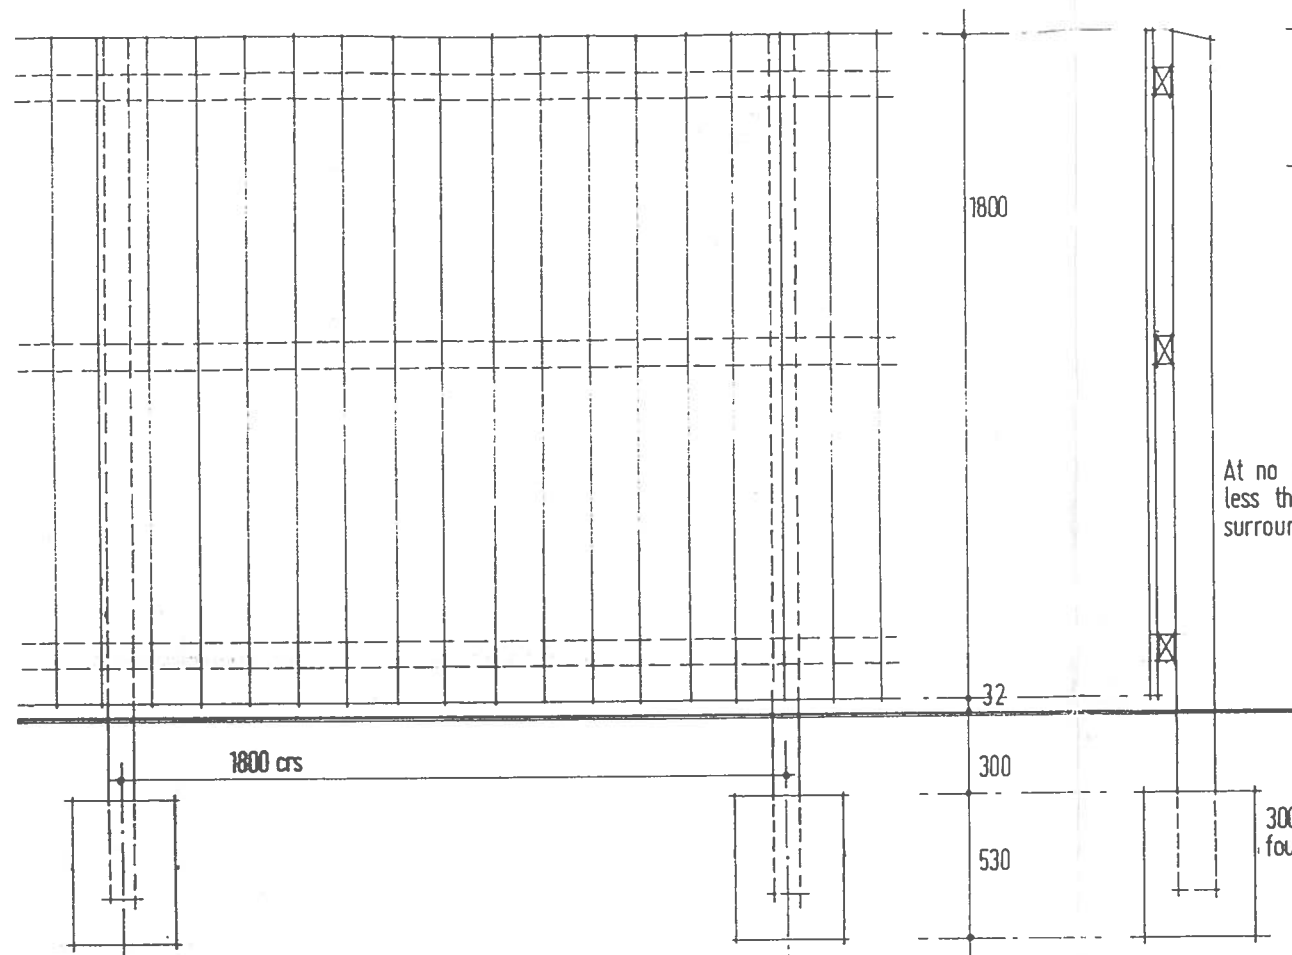

DETAIL OF BOARD 1:1

At no point is the fence to less than 1800 above immediately surrounding ground level.

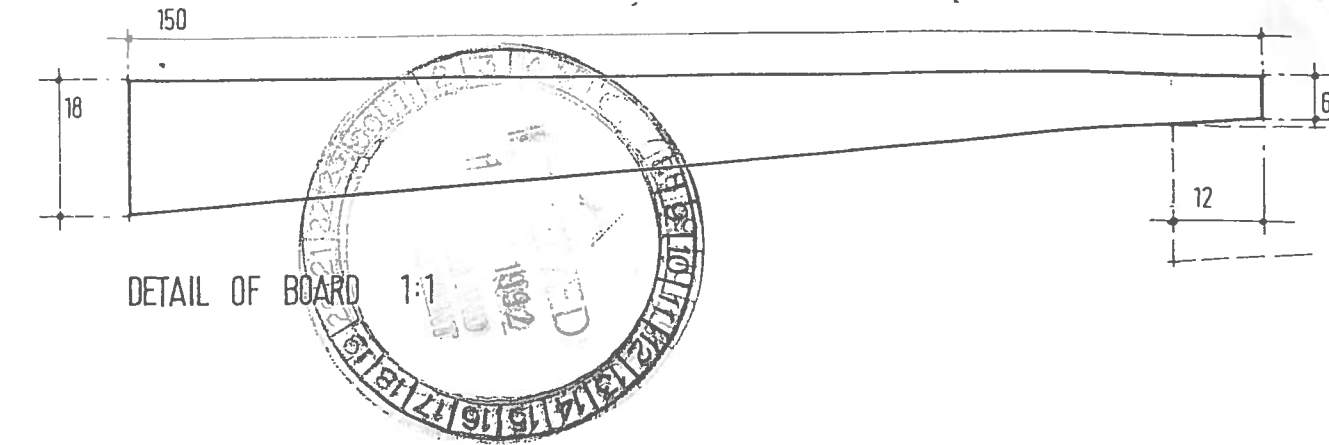

ELEVATION 1:20

SECTION

100x75x2400 long posts

75x50 rails

PLAN 1-2

FORWARD OF THE
VALUATION OF CLAMORGAN
TOWN AND COUNTRY PLANNING ACT, 1990
ALL WORKS SUBJECT TO
COMPLIANCE WITH CONDITIONS IF ANY
- 3 SEP 1992
Chief Planning and Development Officer

REVISIONS

DO NOT SCALE
Dimensions must be verified
by main contractor on site. If
in doubt refer to Architect.

CLIENT

JOB TITLE

DRWG TITLE CLOSE BOARDED TIMBER SCREEN

Drawn pb

Checked

Date


Scale

Joh

Dwg TS.1

R


Wyn Thomas+Partners

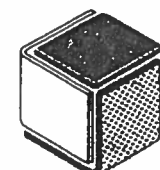




HOUSE TYPES

DENHAM	7
SUTTON	6
DA	3
BUDWORTH	4
	20

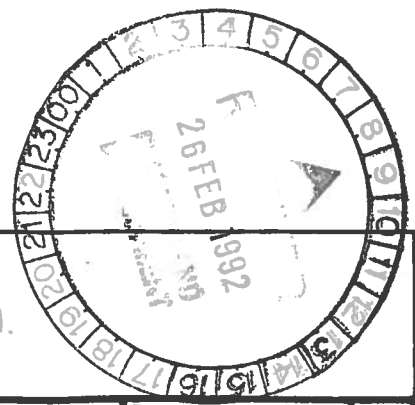

REVISIONS 	CLIENT IDEAL HOMES WALES		Wyn Thomas+Partners 		
	JOB TITLE LLANDOUGH FARM, LLANDOUGH.				
	DRWG TITLE SKETCH LAYOUT.				
Drawn PB	Checked	Date 19.11.91	Scale 1:500	Job	Dwg SK100

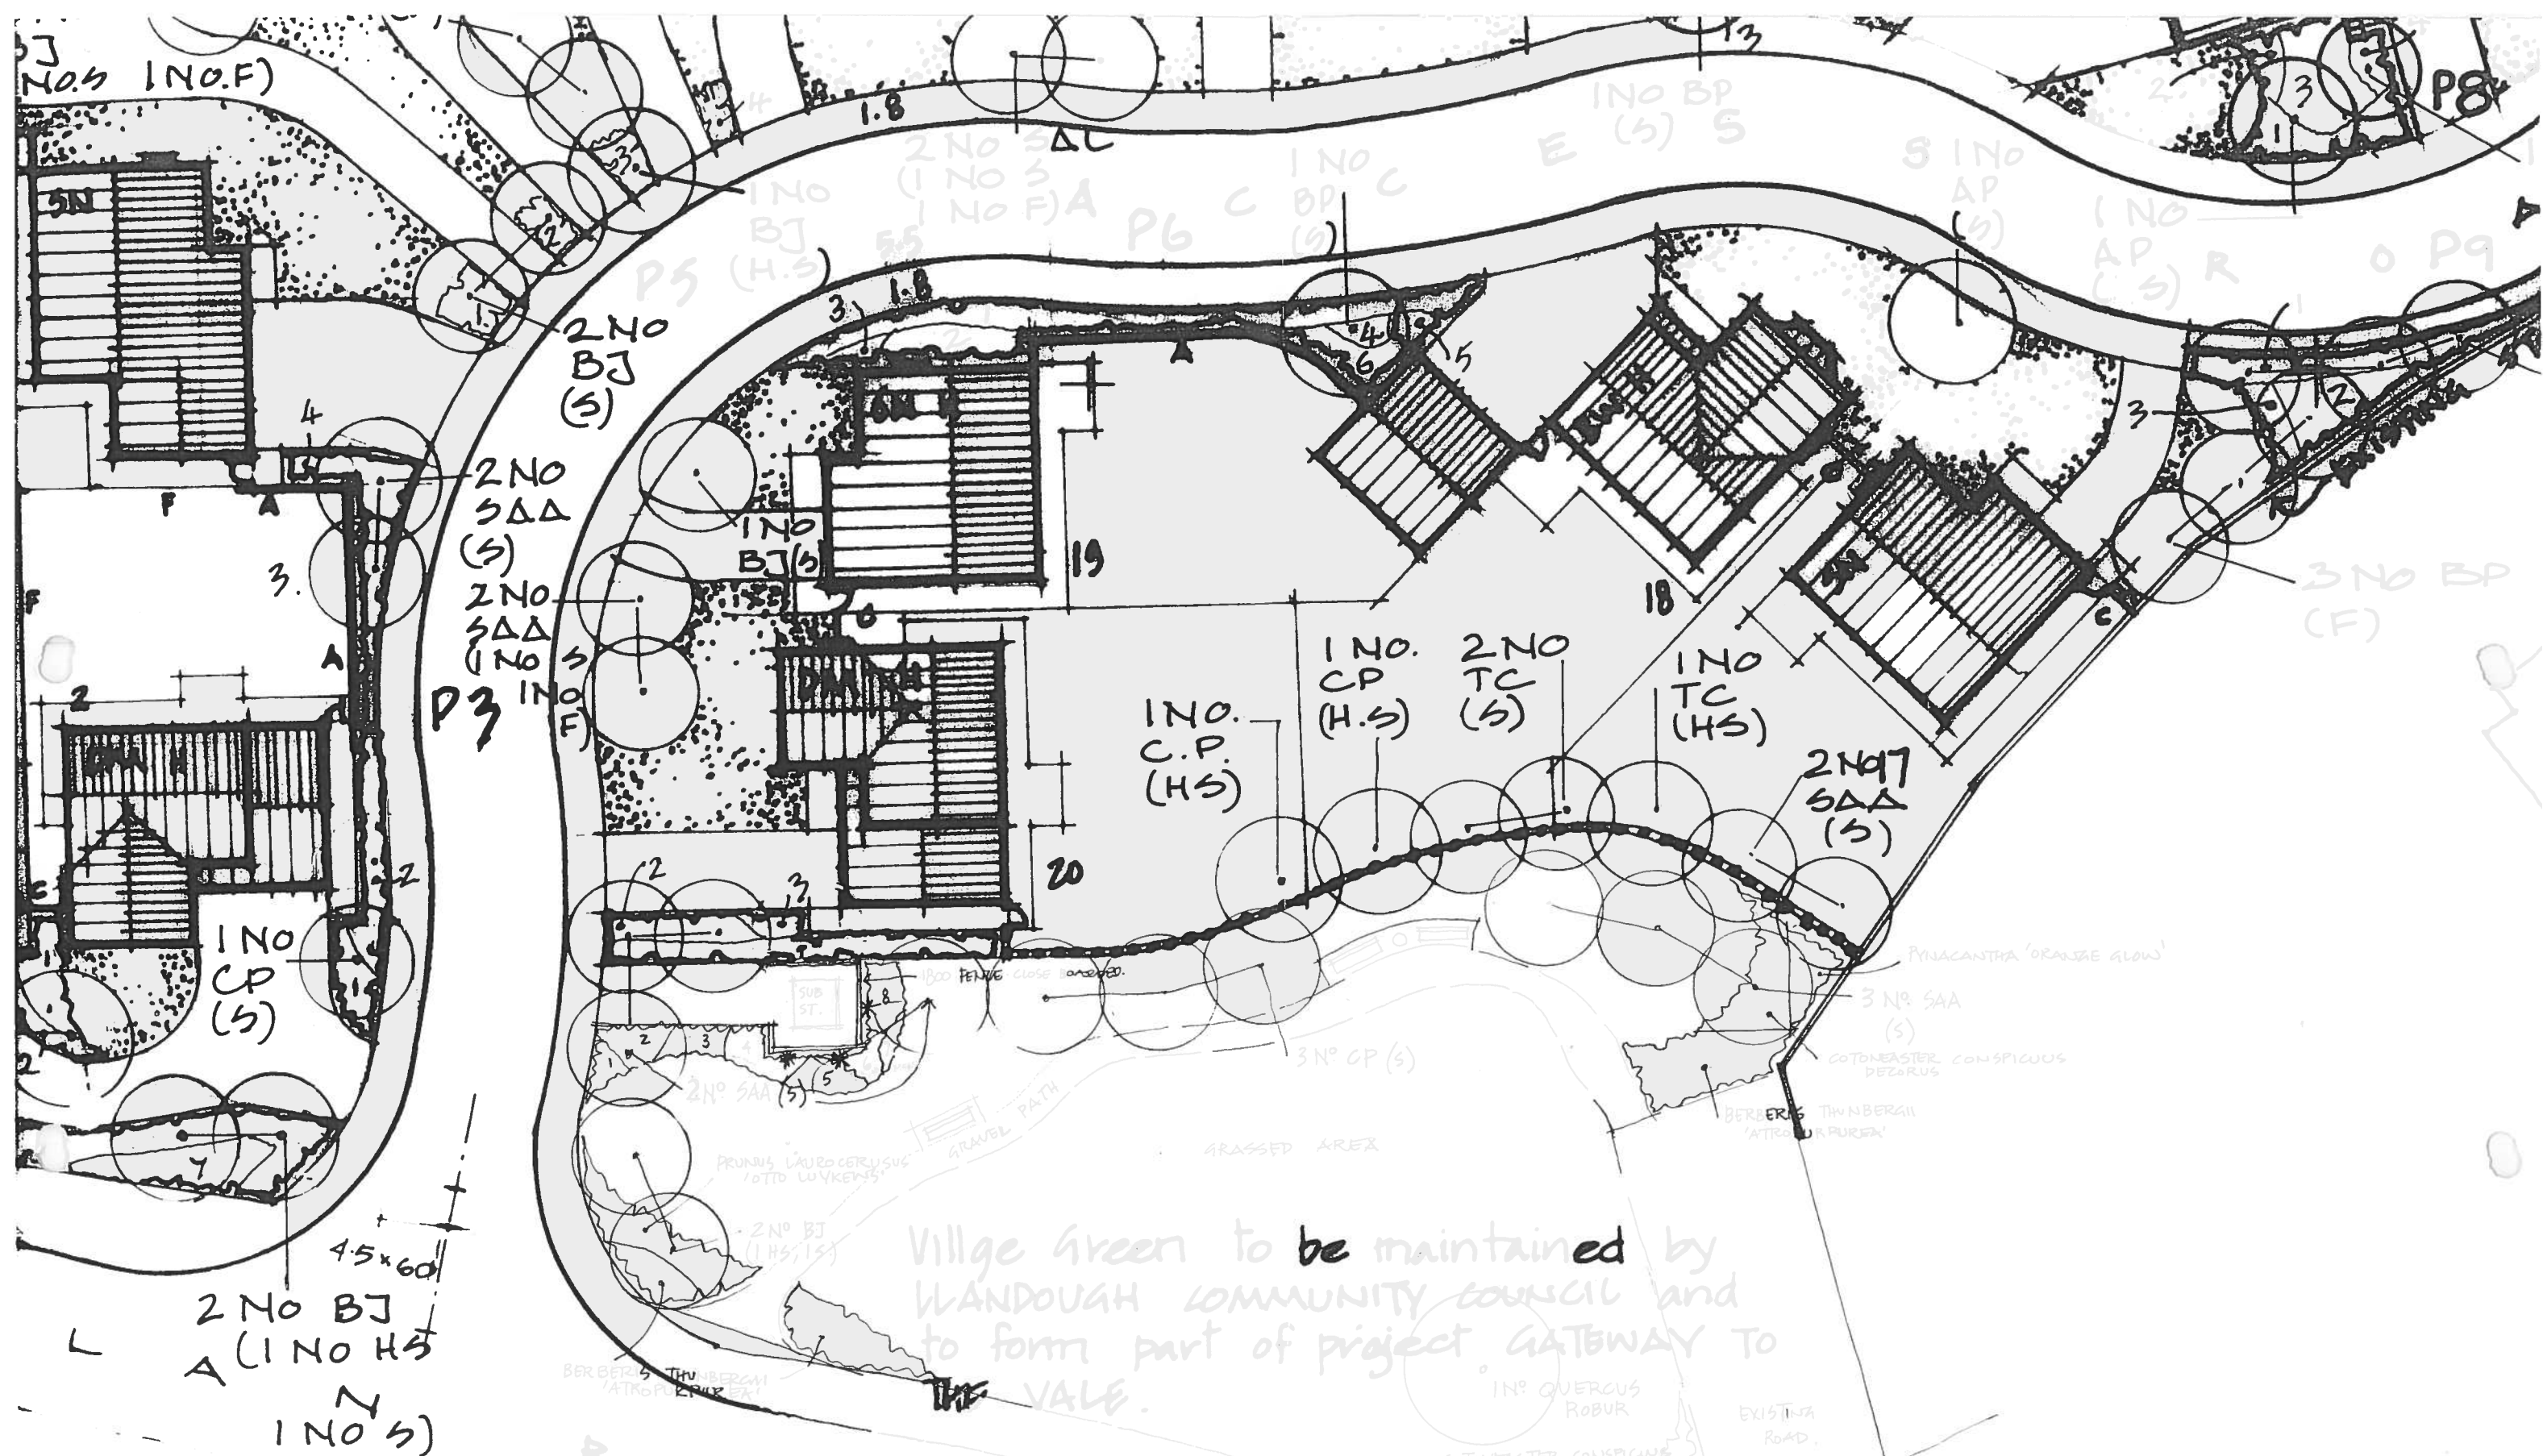

SUB STATION PLANTING.

SHRUBS.

1. STEPHANANDRA 'INOSA CRISPA'
2. COTONEASTER 'CONSPICUOUS DECORUS'
3. ROSA RUGOSA 'FRAU DAGMAR HASTROP'
4. PYRACANTHA 'ORANGE GLOW'
5. POTENTILLA 'TANGERINE'
6. ESCALLONIA 'RONARD SEEDLING'
7. ROSA RUGOSA 'FRAU DAGMAR HASTROP'
8. PYRACANTHA 'ORANGE GLOW'

CLIMBERS.

- *. PARTHENOCLISSUS HENRYANA

HEIGHT (m)	TYPE	QTY (MM)
30-45	C.G. 1.5L	500
30-45	C.G. 2.0L	500
45-60	C.G. 3.0L	750
60-90	C.G. 3.0L	600
30-45	C.G. 3.0L	500
45-60	C.G. 3.0L	750
45-60	C.G. 3.0L	750
60-90	C.G. 3.0L	600

No.	QTY
1	1
2	1
3	1
4	1
5	1
6	1
7	1
8	1

IDEAL HOMES WAVES
WANDOUGH FARM, WANDOUGH
VILLAGE GREEN PLANTING.


3024-VG-01A

Provisional Register Map of Town or Village Green VG 41
This is the first edition of this map.

COMMONS REGISTRATION ACT 1965
SOUTH GLAMORGAN COUNTY COUNCIL
REGISTRATION AUTHORITY
16 JUN 1970


embayce

M.D. BOYCE, COUNTY SOLICITOR
For and on behalf of South
Glamorgan County Council.

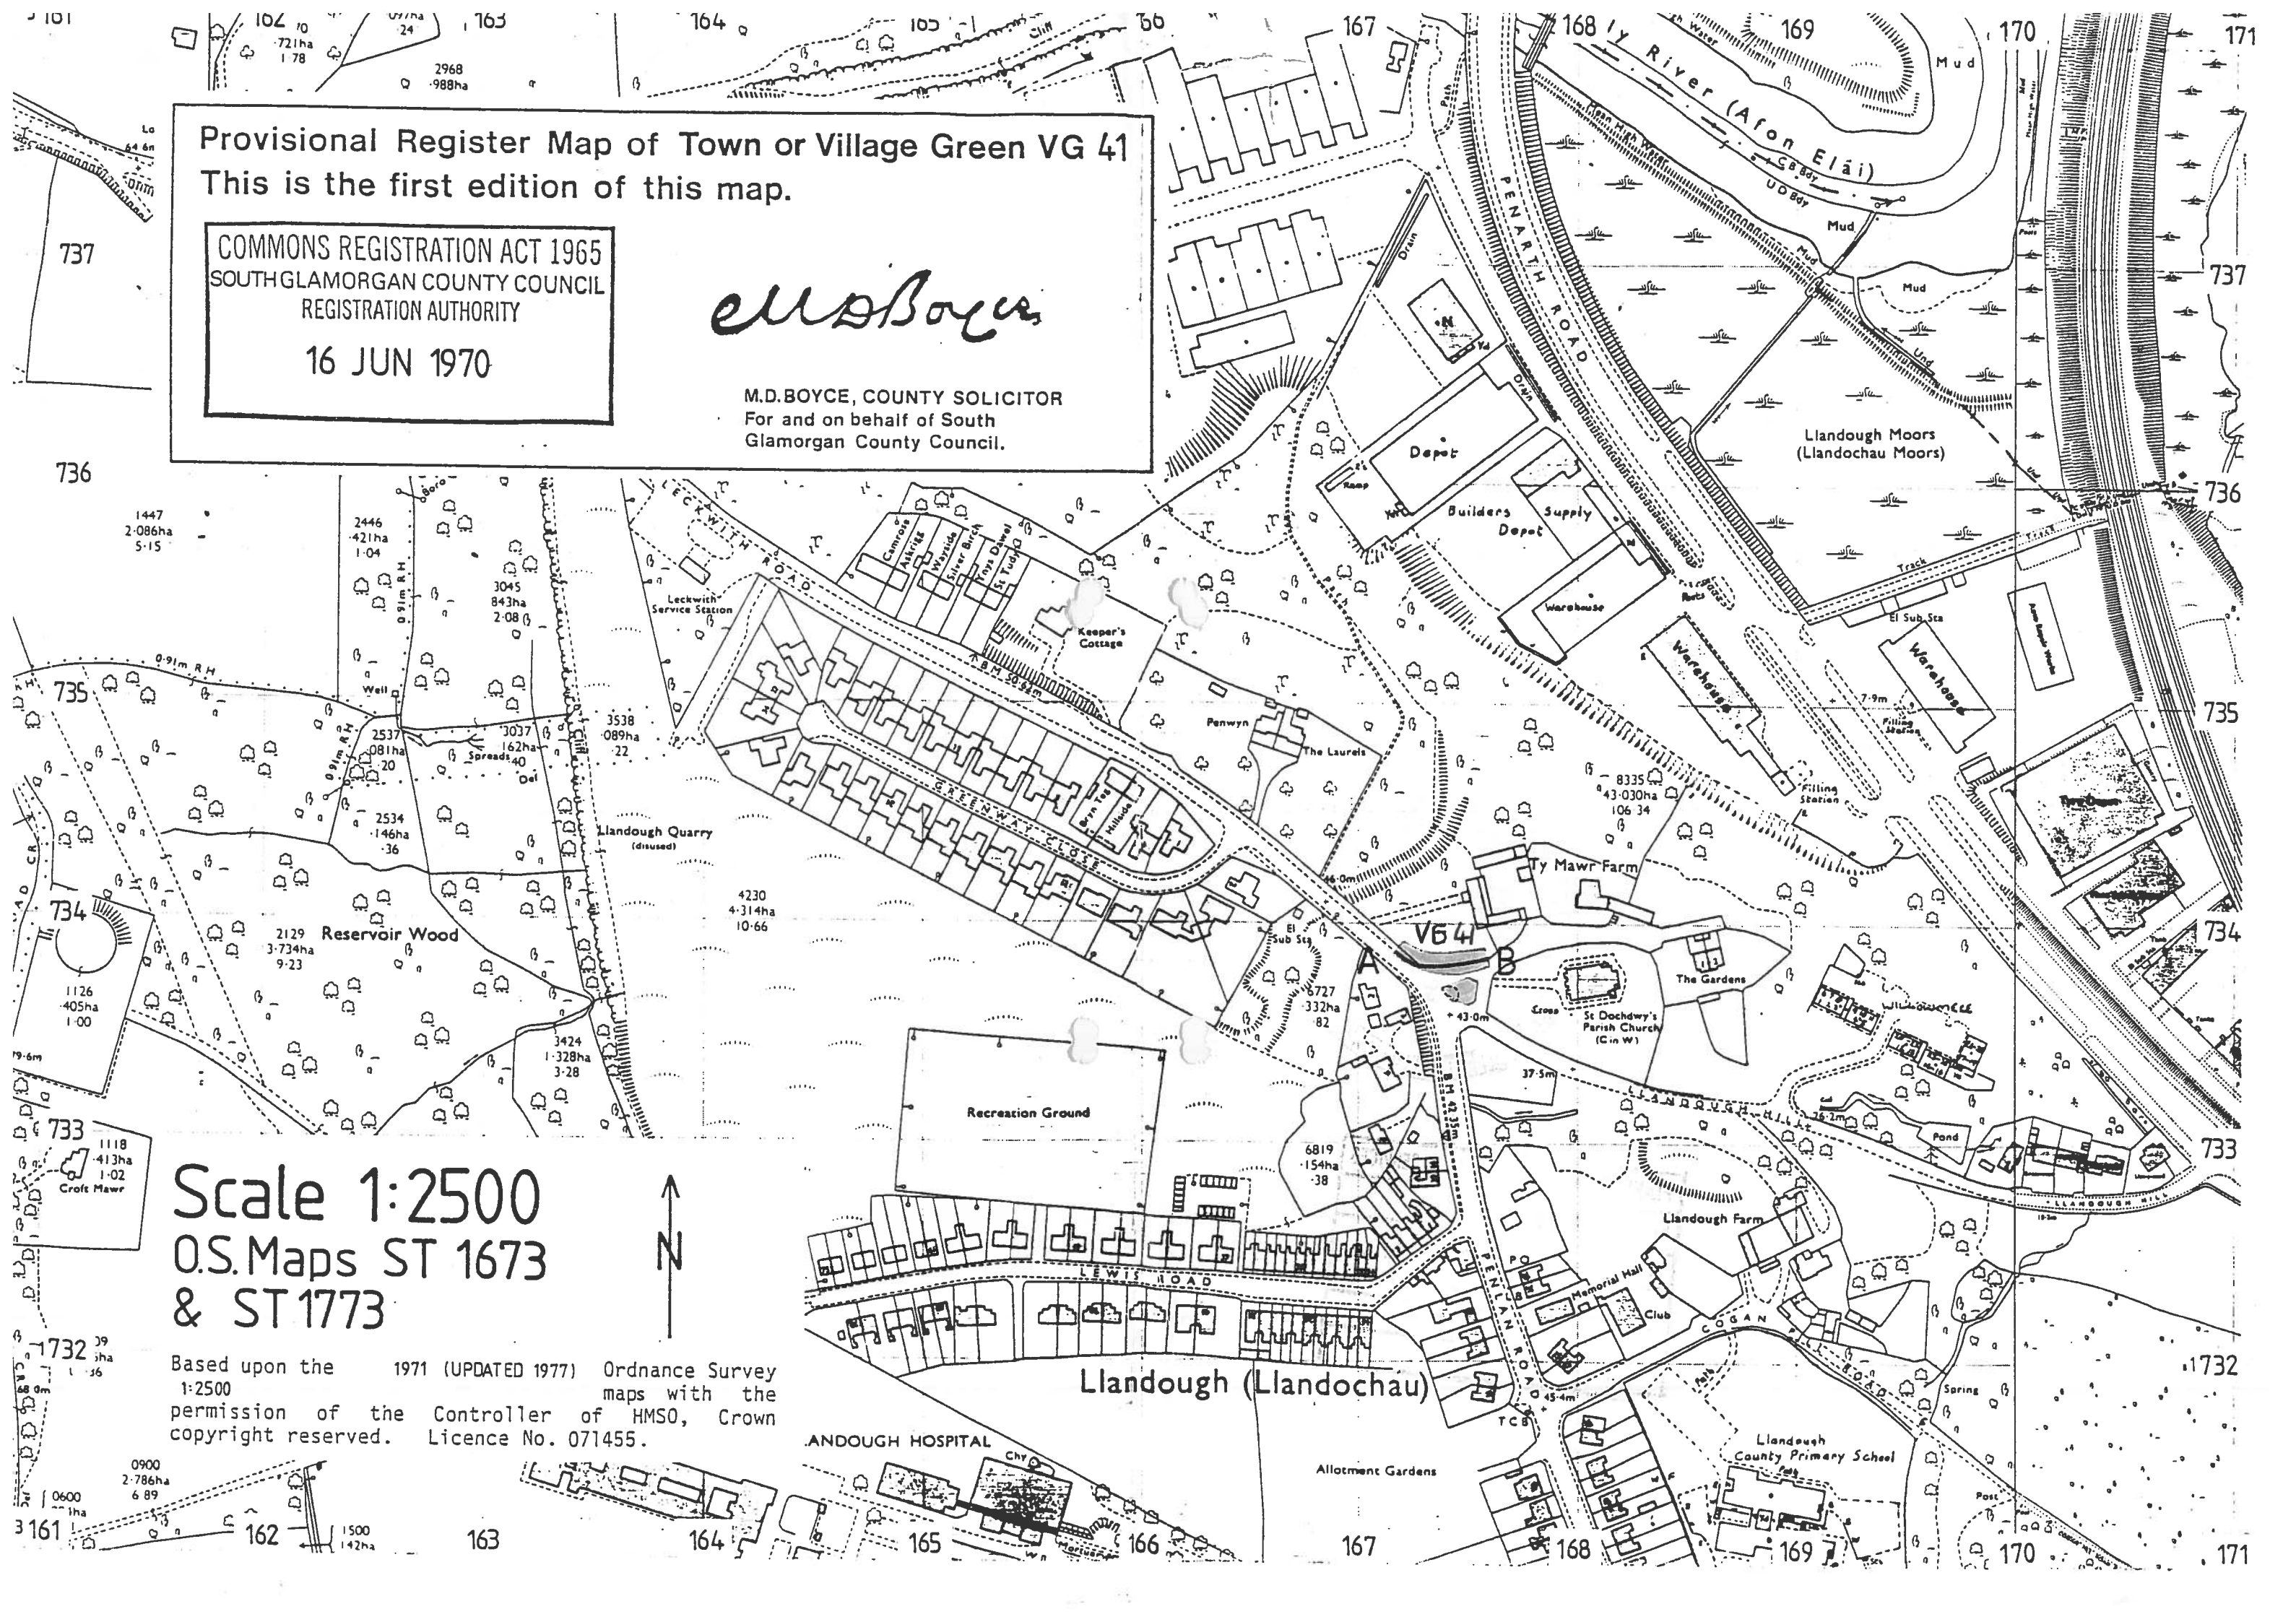

Scale 1:2500
O.S. Maps ST 1673
& ST 1773

Based upon the 1971 (UPDATED 1977) Ordnance Survey maps with the permission of the Controller of HMSO, Crown copyright reserved. Licence No. 071455.

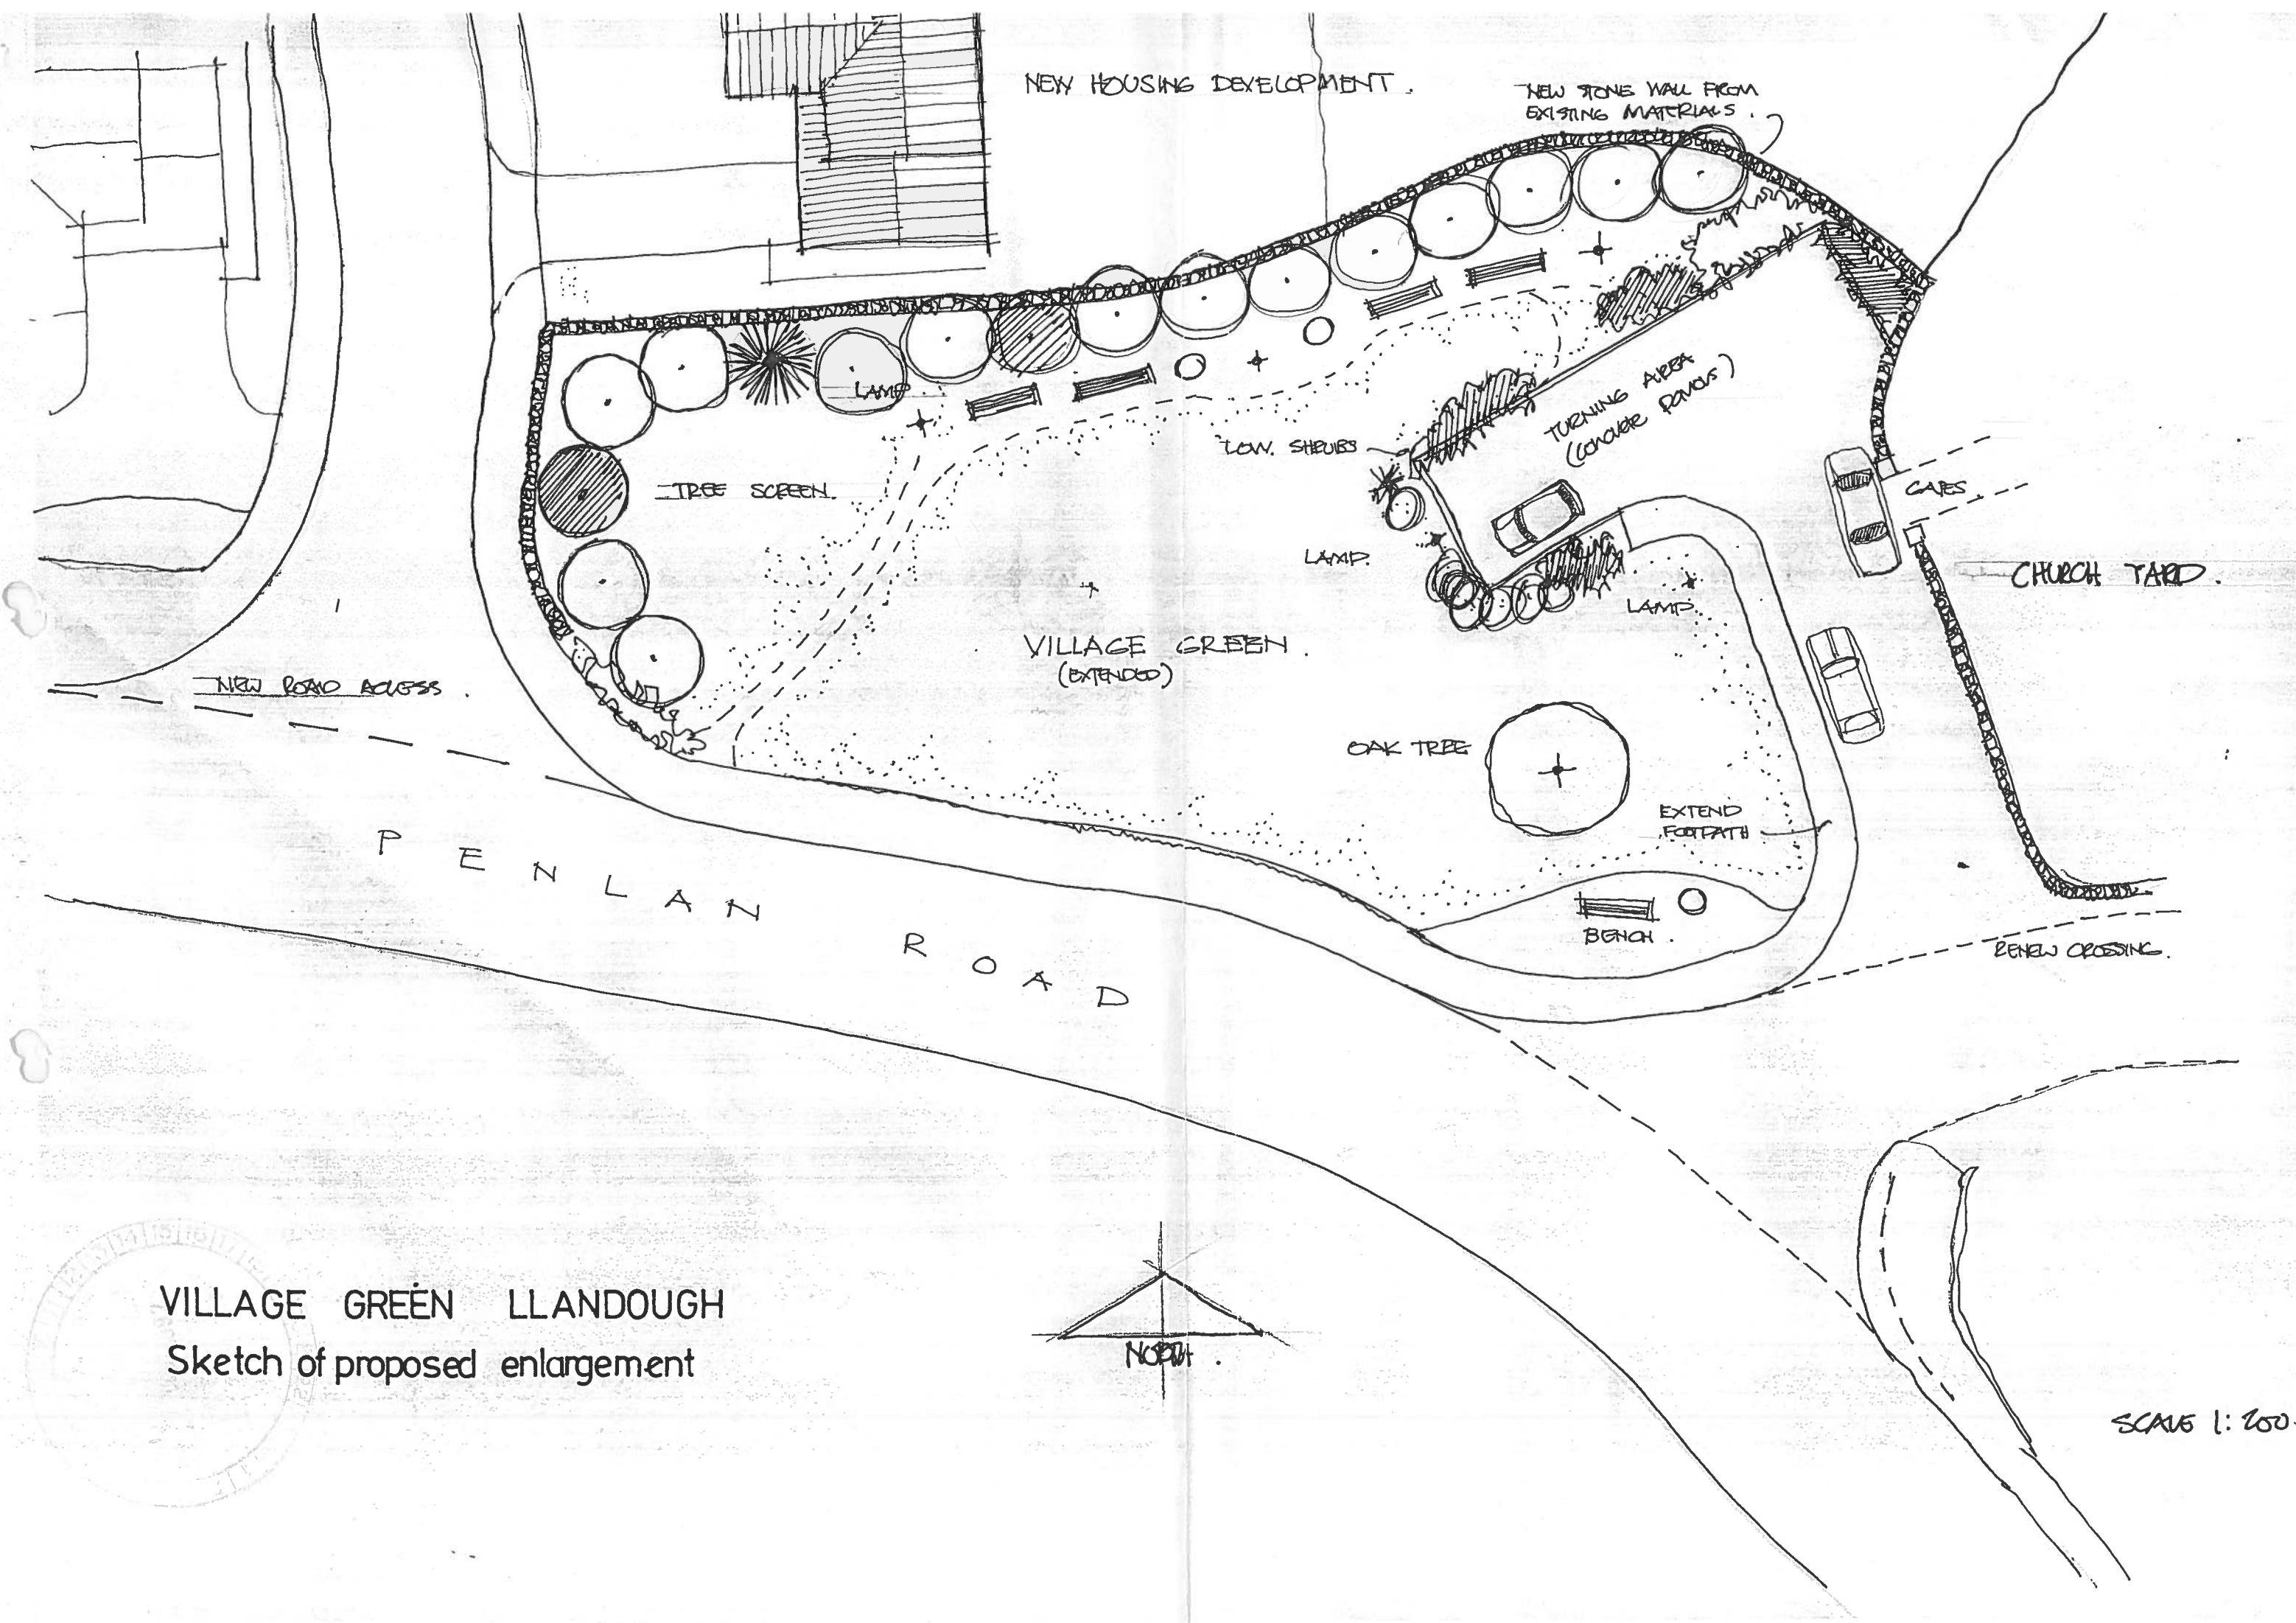

VILLAGE GREEN LLANDOUGH
Sketch of proposed enlargement

SCALE 1:100.